

GENERAL NOTES:

1.

PROPERTY OWNER:KASTELBERG ELIZABETH S. 6107 BAT ST, RICHMOND,VA 23226

2.

PARCEL ID GPIN#: W0210305008

3.

DISTRICT: WESTHAMPTON TERRACE

4.

ZONING: R-4 - Residential (Single Family)

5.

WATER: COUNTY

6.

SEWER: SEPTIC

7.

LAND AREA: 0.2479 ACRES

CODES:

International Residential Building Code

2021

Virginia Uniform Statewide Building Code

2021

Frost Depth

18 inches

Design Wind Speed


115 mph, 3-second gust


Snow Load

20 psf

Seismic Design Category

C

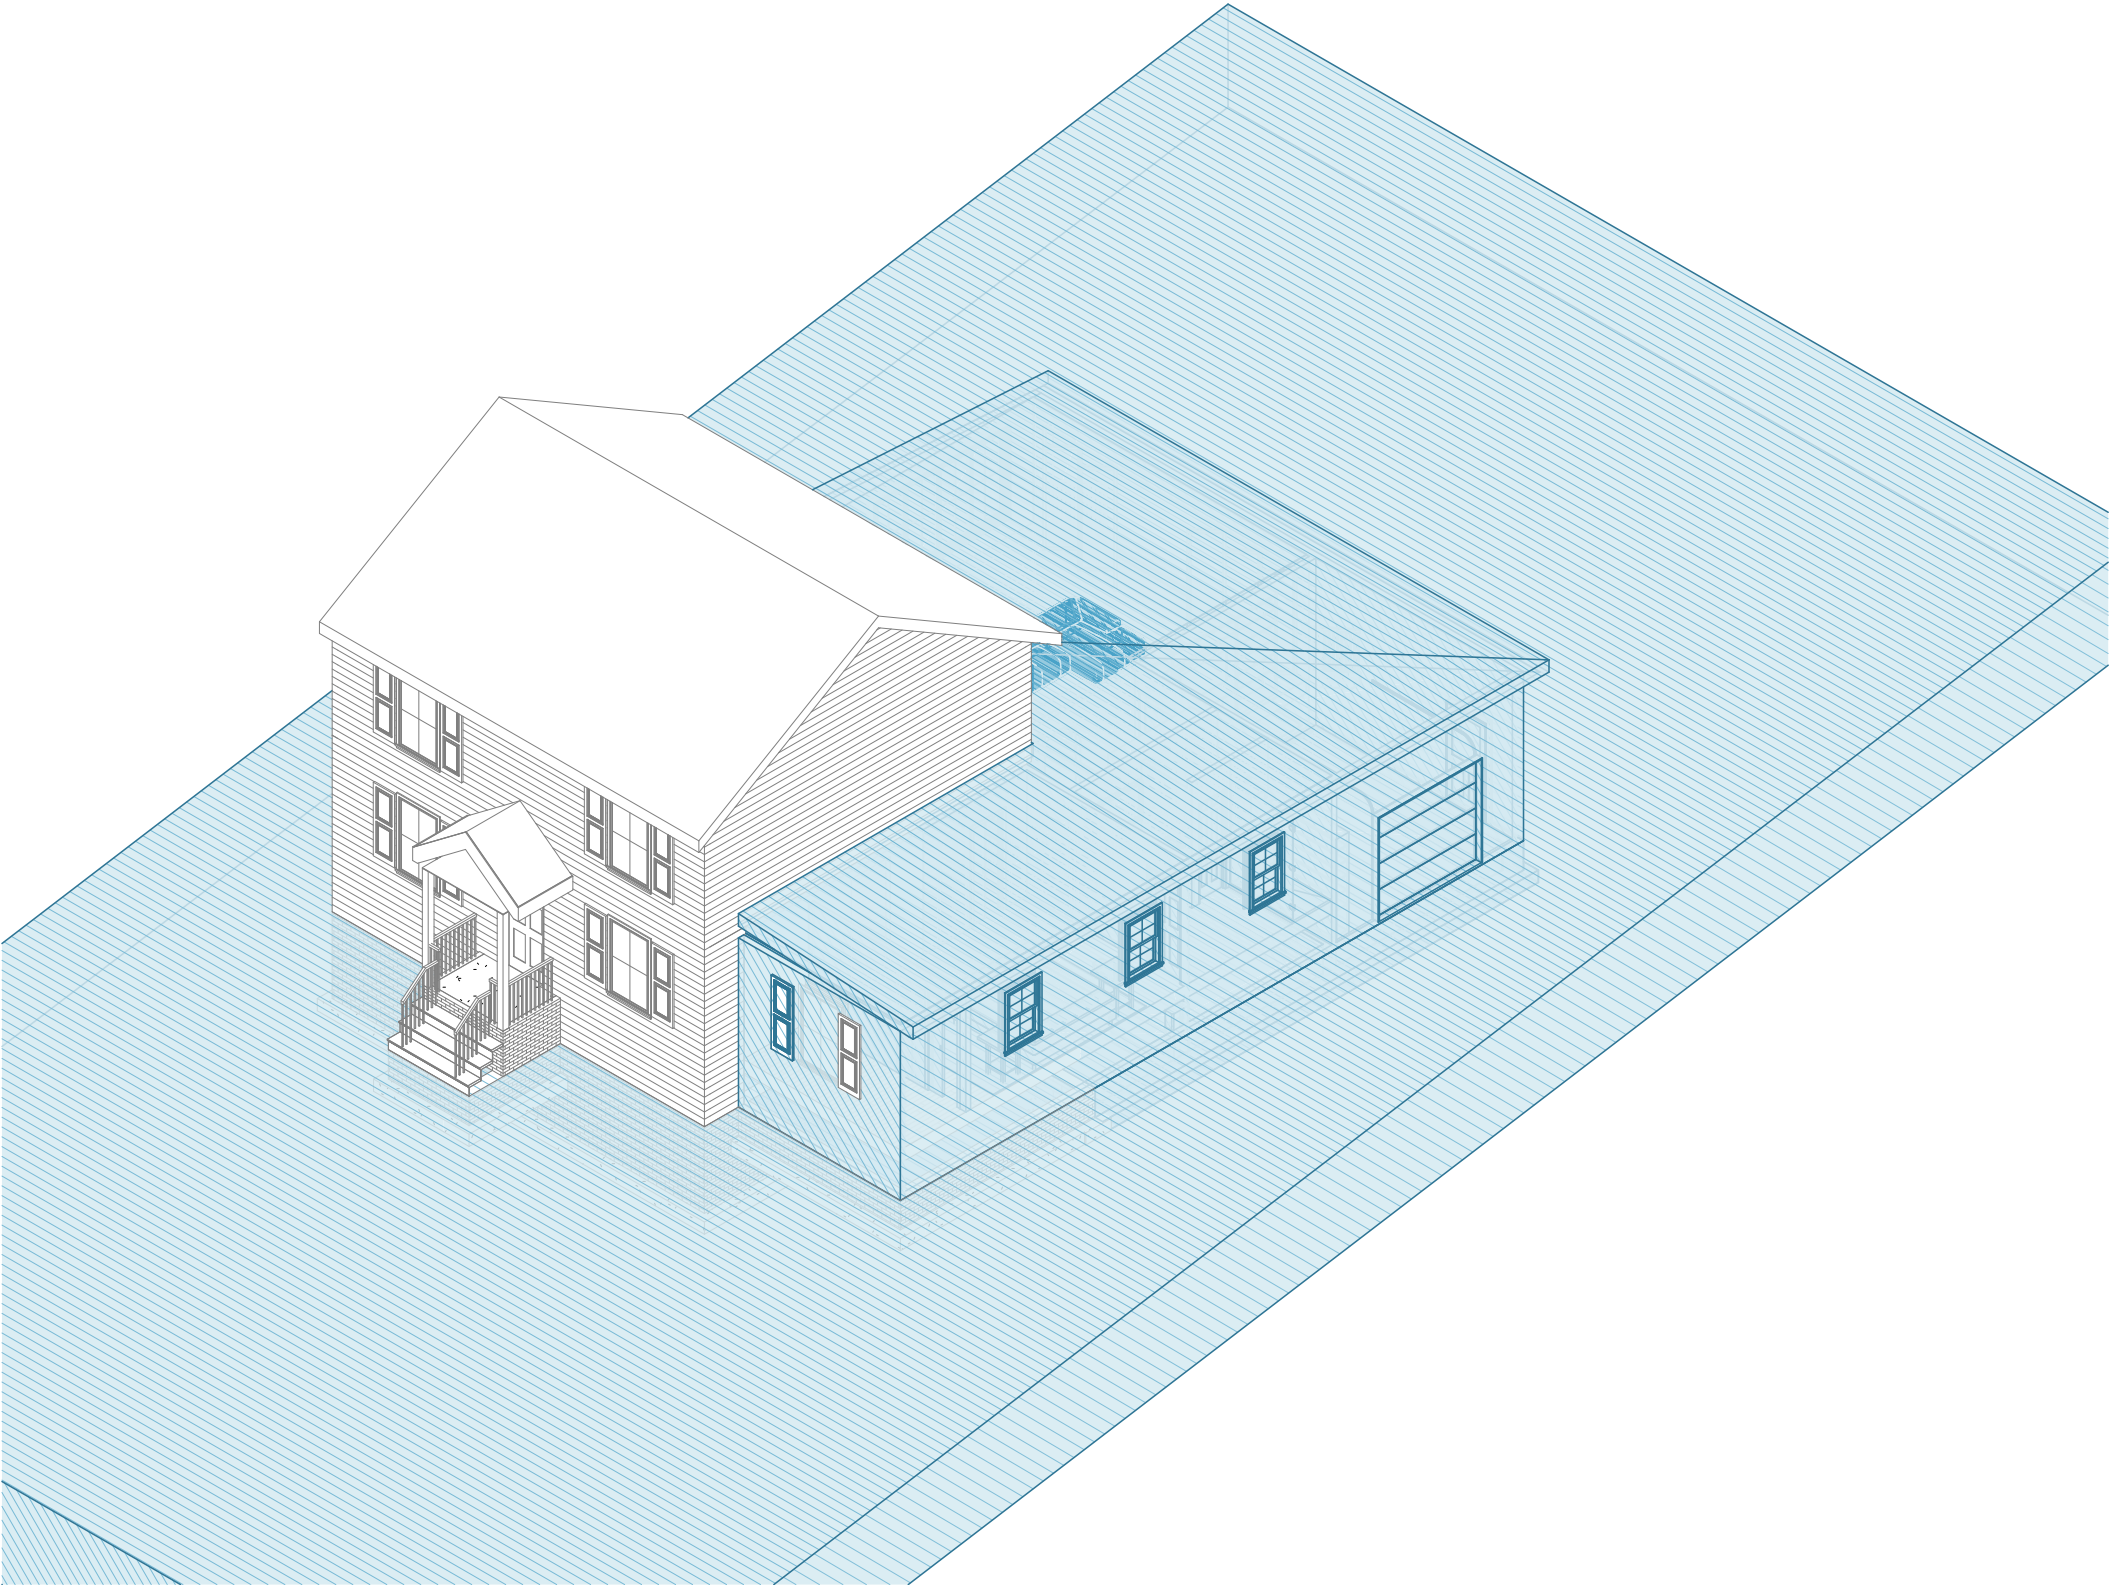


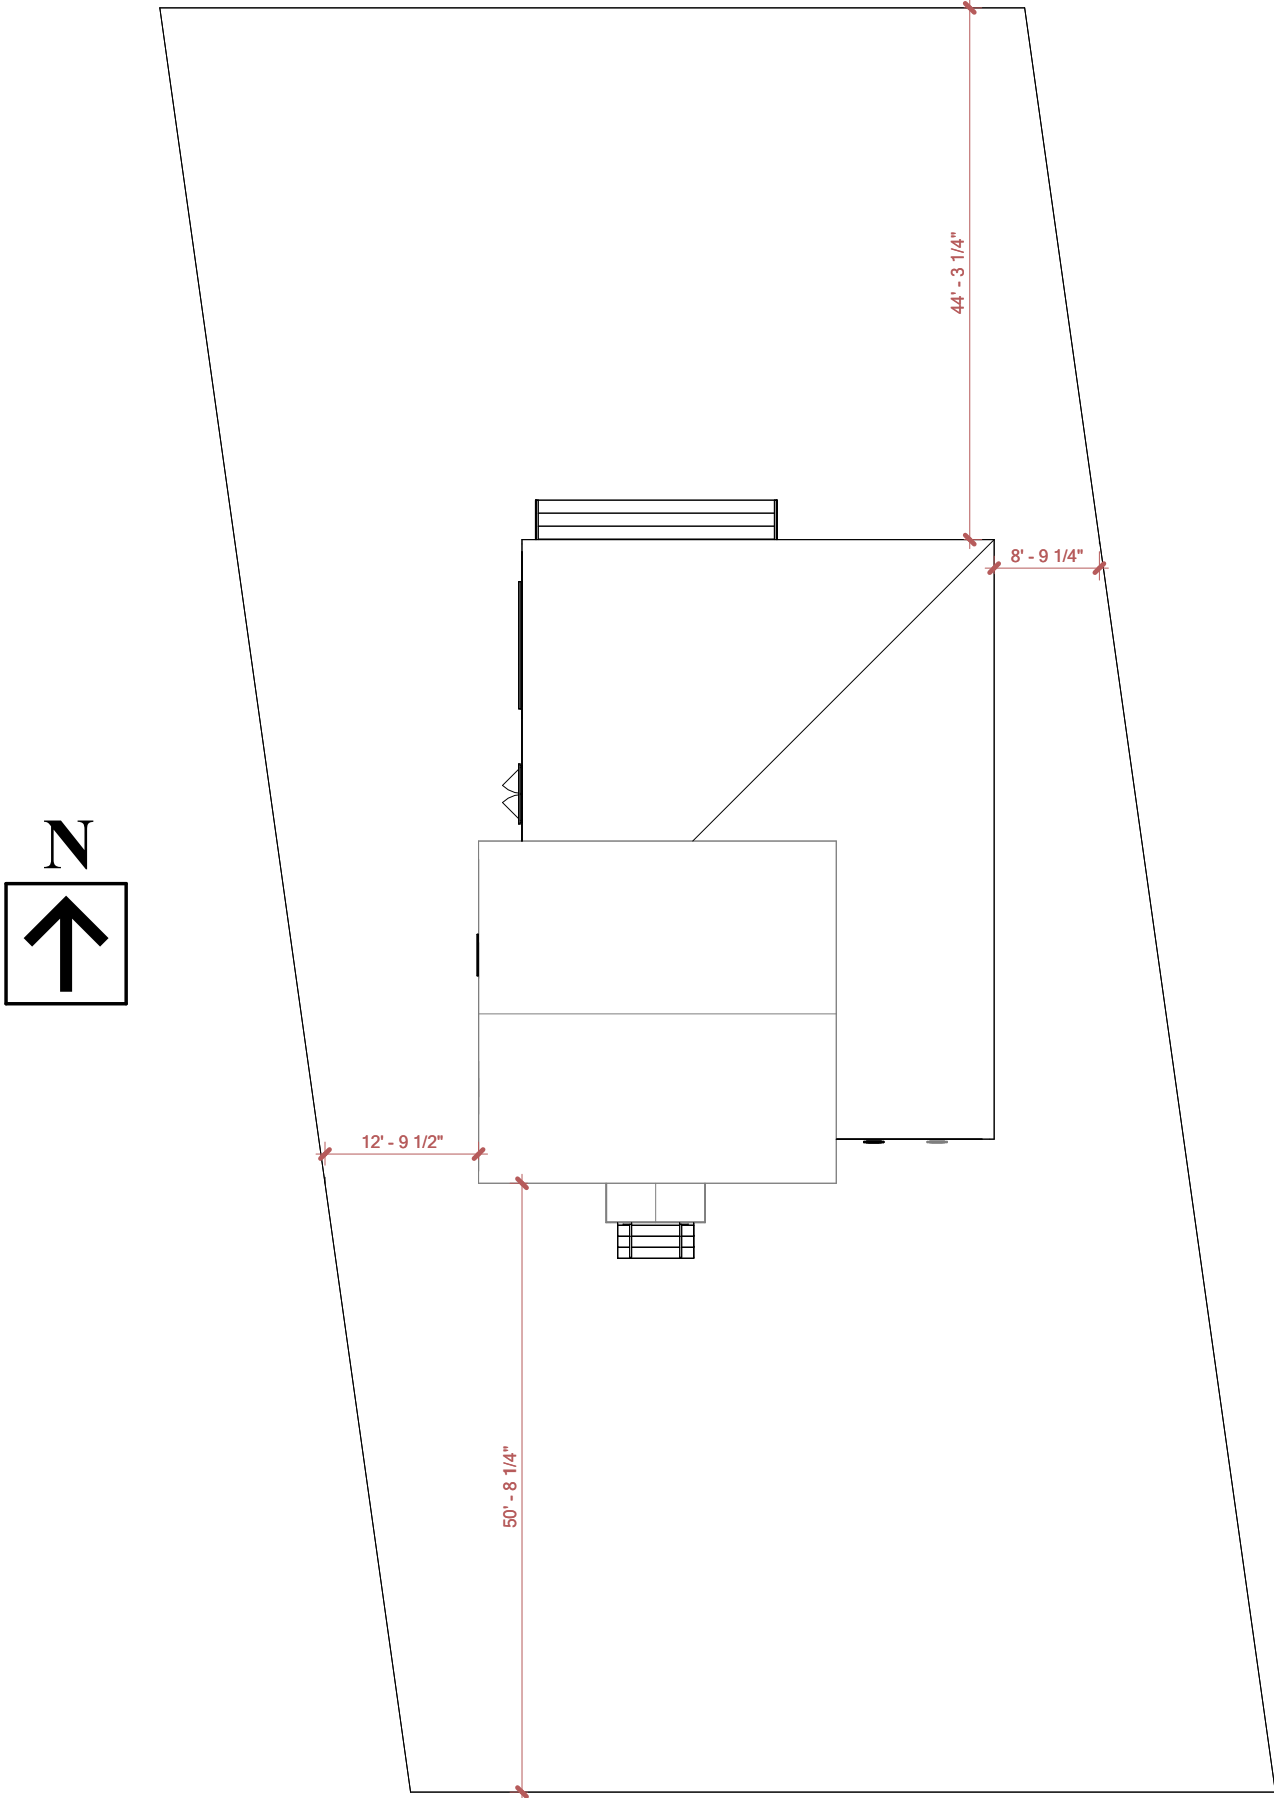

1

SITE PLAN

1/16" = 1'-0"

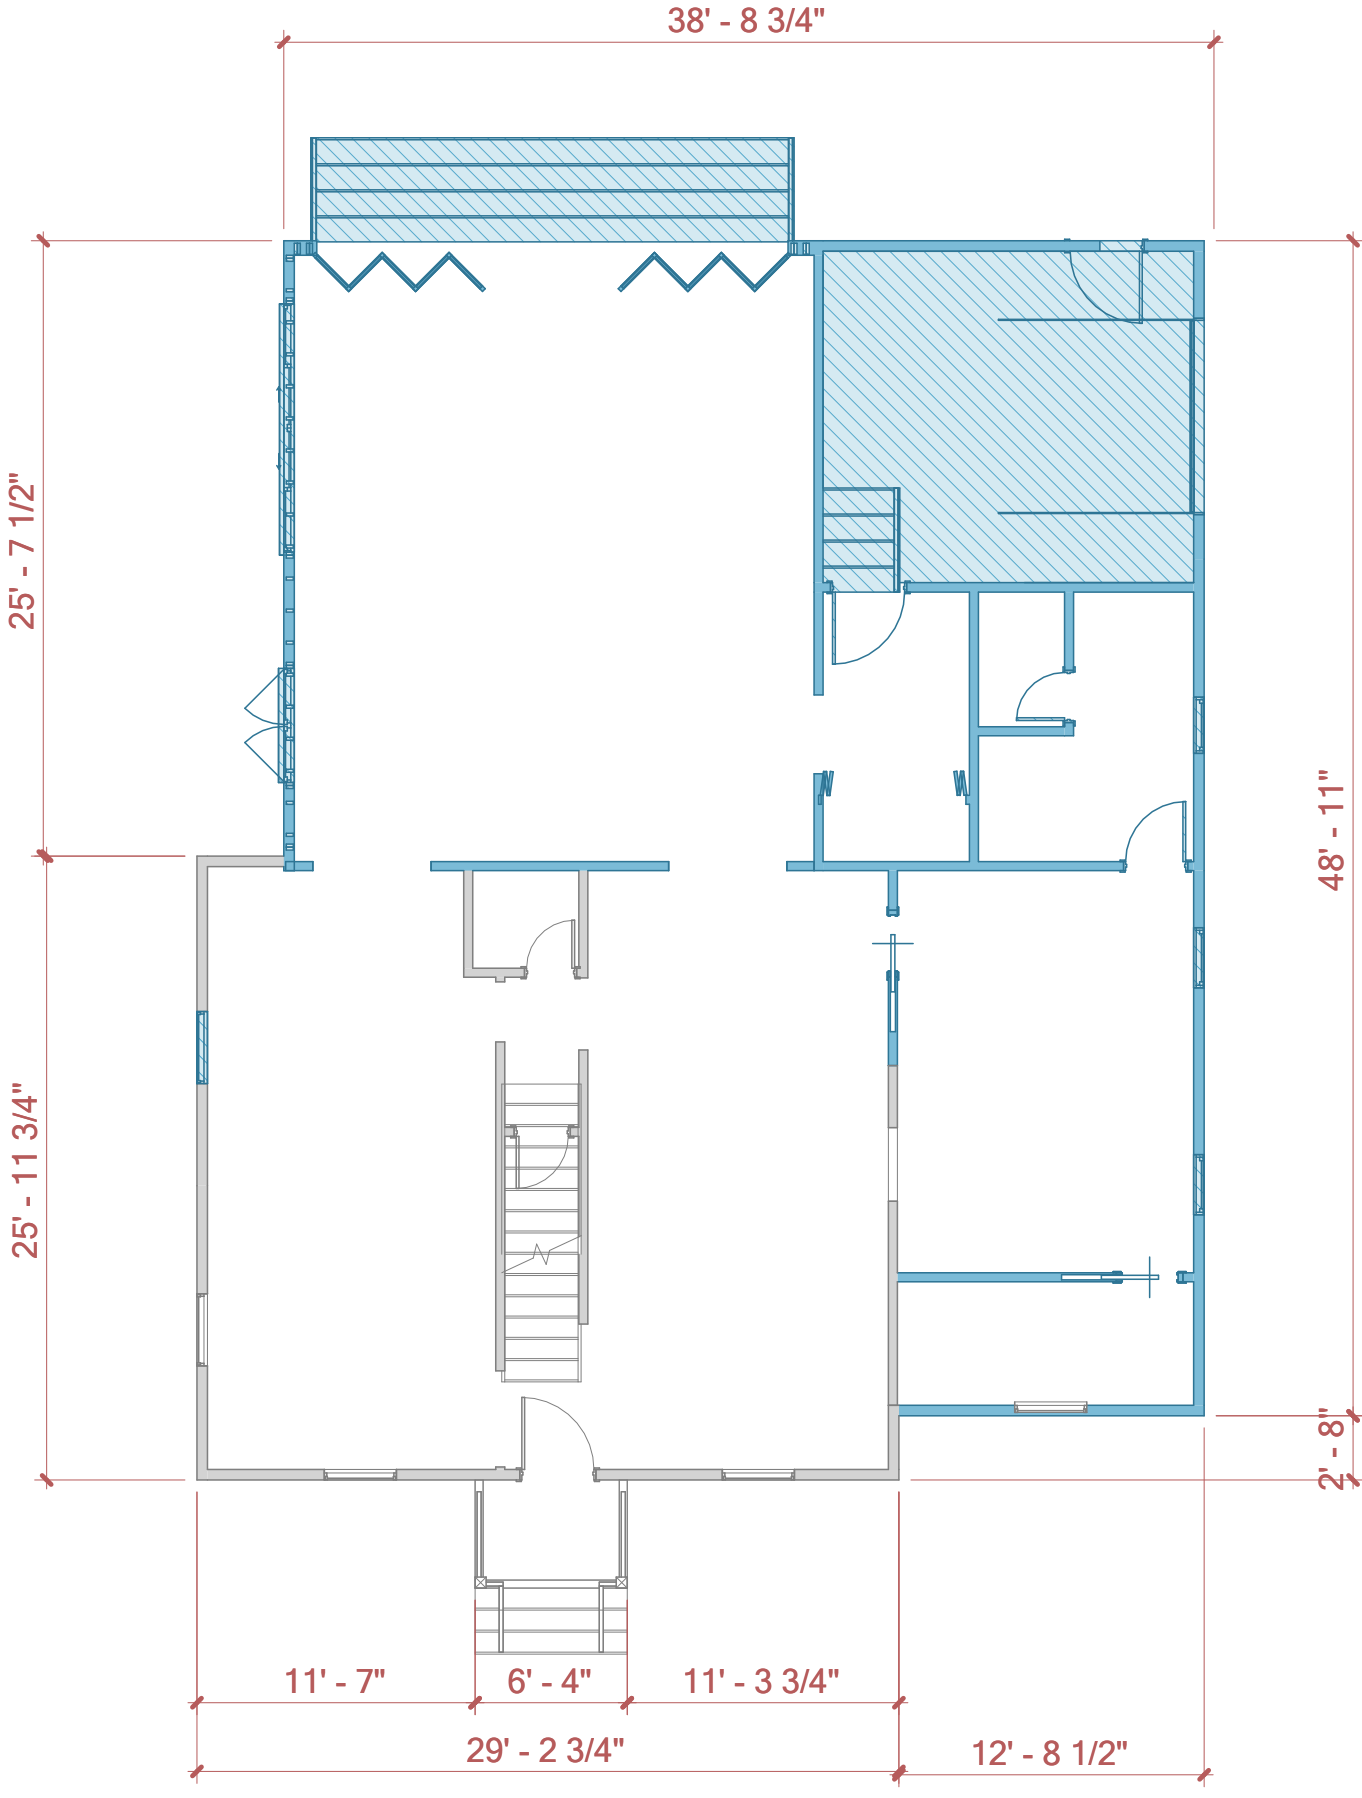

3

BLUEPRINT

1/8" = 1'-0"

GENERAL DRAWING NOTES:

1) INFORMATION ON PLANS SUPERCEDES GENERAL NOTES

2) ALL WORK SHALL CONFORM WITH ALL GOVERNING LAWS, CODES AND ORDINANCES INCLUDING, BUT NOT LIMITED TO, THE VIRGINIA UNIFORM BUILDING CODE & THE INTERNATIONAL RESIDENTIAL CODE (2018).

3) ALL TRADES SHALL FURNISH ALL LABOR, MATERIALS & PERFORM ALL WORK NECESSARY, INDICATED OR REASONABLY INFERRED OR REQUIRED BY ANY CODE W/ JURISDICTION TO COMPLETE THEIR SCOPE OF WORK.

4) VERIFY ALL FIELD CONDITIONS & PLANS. CONTACT CONSTRUCTION SUPERVISOR IMMEDIATELY WITH ANY CONFLICTS BETWEEN THESE PLANS & EXISTING FIELD CONDITIONS BEFORE BEGINNING TO WORK.

5) IT IS THE CUSTOMER'S RESPONSIBILITY TO PROVIDE ALL WATER & SEWER CONNECTIONS TO THE RESIDENCE. PLEASE COORDINATE IN ADVACE ALL FEES, APPLICATIONS & AUTHORITIES INVOLVED IN THE CONNCTECTION OF WATER AND SEWER.

6) CONTRACTOR IS RESPONSIBLE TO VERIFY PLAN, EXISTING DIMENSIONS AND CONDITIONS OF PROPOSED DESIGN.

7) THE CONTRACTOR IS SOLELY RESPONSIBLE FOR ALL CONSTRUCTION MEANS, MATERIALS AND METHODS, ENSURING THAT PROJECT COORDINATION IS IN ACCORDANCE WITH REQUIREMENTS OF THE AUTHORITY HAVING JURISDICTION.

STRUCTURAL SPECIFICATIONS:

1) THE CONDITIONSAND ASSUMPTIONS STATED IN THESE SPECIFICATIONS SHALL BE VERIFIED BY THE CONTRACTOR FOR CONFORMANCE TO ALL CODES AND CONDITIONS. IN THE EVENT OF ANY DISCREPANCY BETWEEN THESE SPECIFICATIONS AND CODES AND CONDITIONS, THE CONTRACTOR SHALL NOTIFY THE BUILDER IN WRITING OF THE DISCREPANCY AND ALTERNATE PRESCRIPTIVE MEASURES OR ENGINEERED SOLUTIONS SHALL BE APPLIED TO ENSURE STRUCTURAL ADEQUACY.

2) WHERE A CONFLICT BETWEEN THESE DRAWINGS EXISTS WITH AFOREMENTIONED CODE OR DESIGN PRINCIPLES, THE MORE STRINGENT REQUIREMENT SHALL BE FOLLOWED.

3) SOILS SHALL PROVIDE AN ASSUMED 1500 LBS. ALLOWABLE BEARING. THE WATER TABLE (SEASONAL OR OTHERWISE) SHALL NOT EXTEND TO WITHIN 2' OF THE BOTTOM OF CONCRETE SLABS, FOOTINGS AND WALLS. FOOTINGS MUST EXTEND TO FROST DEPTH DESIGNATED BY THE AUTHORITY HAVING JURISDICTION.

4) FOOTINGS SHALL BE PLACED ON NON-EXPANSIVE SOILS.

5) ALL STRUCTURAL WALL SHEATHING SHALL BE 1/2" O.S.B AND FASTED IN ACCORDANCE WITH TABLE 602.10.4

6) BACK FILL FOR SLABS MUST BE IN ACCORDANCE WITH IRC R506.

7)STRUCTURAL FLOOR SHEATHING SHALL BE MINIMUM 3/4" O.S.B TONGUE AND GROOVE OR BLOCKED AT ALL EDGES, FASTEN WITH 8D COMMON NAILS FASTED 6" AT EDGES 12" AT INTERMEDIATE SUPPORT

WOOD:

1) ALL SOLID SAWN HEADERS, BEAMS AND GIRDERS SHALL BE MINIMUM SYP #2, APPLY WET FACTOR FOR WEATHER EXPOSED MEMBERS.

2) WOOD TRUSSES SHALL BE DESIGN INSTALLED AND MANUFACTURED IN ACCORDANCE WITH ANSI TP1. MANUFACTURER SHALL PROVIDE SEALED TRUSS DRAWINGS FOR REVIEW AND INSPECTION.

3) ALL WOODEN MEMBERS SHALL BE PROTECTED FROM DECAY AND TERMITE INFESTATION IN ACCORDANCE WITH R317 AND R318 OF THE IRC.

4) PROVIDE A CONTINUOUS DOUBLE TOP PLATE ACROSS ALL BEARING STUD WALLS.

5) MINIMUM COLUMN SUPPORT UNDER ANY BEAM OR HEADER UNLESS OTHERWISE NOTED IS A SINGLE 2X4 SPF #2. HEADERS MUST HAVE A MINIMUM OF 1 JACK STUD AND 1 KING STUD.

6) FOUNDATION ANCHORAGE SHALL BE IN ACCORDANCE WITH R403.1.6.

7) ALL POSTS SHOWN ON FLOOR OR FRAMING PLAN SHALL TERMINATE TO FOOTING AT GROUND OR TRANSFER TO A BEAM BELOW.

8) ALL STRUCTURAL COMPOSITE LUMBER SHALL BE INSTALLED IN ACCORDANCE WITH MANUFACTURER'S SPECIFICATIONS AND MUST BE ACCOMPANIED BY BOTH A LAYOUT AND BEAM SHEETS PRODUCED BY DESIGNER.

9) BORING/NOTCHING LIMITS SHALL NOT EXCEED MANUFACTURER'S SPECS FOR STRUCTURAL COMPOSITE NOR IRC LIMITS FOR SOLID SAWN LUMBER.

10) ALL WALLS TO BE ASSEMBLED IN ACCORDANCE WITH FLOOR PLAN AND FRAMING PLANS REFERENCED HERE.

SAFETY:

1) ALL HANDRAILS AND GUARD RAILS ARE TO BE INSTALLED IN ACCORDANCE WITH R311 AND R312.

2) SMOKE ALARMS SHALL BE LOCATED AND INSTALLED ACCORDING TO IRC R314.

3) CARBON MONOXIDE ALARMS, WHEN REQUIRED, SHALL BE LOCATED AND INSATLLED IN ACCORDANCE WITH IRC R315.

4) GLAZING IN HAZARDOUS LOCATIONS, AS SPECIFIED IRC R308, SHALL BE ASSEMBLED AND IDETIFIED WITH A MANUFACTURER'S DESIGNATION SPECIFYING WHO APPLIED THE DESIGNATION AND THE STANDARD WITH WHICH IT COMPLIES, ALTERNATIVE CERTIFICATION MAY BE CONSIDERED BY THE BUILDING OFFCIAL.

5) THE INFORMATION, PLANS AND SPECIFICATIONS APPEARING IN THESE DRAWINGS ARE THE PROPERTY OF 16-32 DRAFTING, LLC. DUPLICATION IN WHOLE OR PART IS PROHIBITED.

ENERGY, THERMAL & MOISTURE:

1) WHERE REQUIRED, WALLS SHALL BE DAMPED-PROOFED/ WATER PROOFED IN ACCORDANCE WITH IRC R405 & R406.

2) A 6 MIL POLYETHYLENE VAPOR RETARDANT SHALL BE PLACED BENEATH ALL INTERIOR SLABS.

3) THE EARTH ENCLOSED BY CRAWL SPACES SHALL BE COVERED WITH A CLASS I VAPOR RETARDANT IN ACCORDANCE WITH IRC R408.

4) FLASHING SHALL BE INSTALLED ON ALL EXTERIOR WALLS TO ENSURE AGAINST WATER FILTRATION, ALL AREAS SPECIFIED IN IRC R703.4 SHALL BE ADDRESSED AS SPECIFIED.

5) AN APPROVED WATER RESISTIVE BARRIER SHALL BE APPLIED TO ALL EXTERIOR SHEATHING, EITHER TYPE I #15 ROOF FELT OR OTHER LISTED AND APPROVED HOUSE WRAP WILL SATISFY THIS REQUIREMENT. INSTALLATION, LAPS, JOINTS AND SEAMS SHALL BE INSTALLED IN ACCORDACE WITH IRC R703.2 OR MANUFACTURER INSTALLATION INSTRUCTIONS.

MASONRY:

1) MORTAR USED SHALL BE TYPE "S" ANY ADDITIVES SHALL BE PROPORTIONED IN ACCORDANCE WITH ASTM C-270.

2) BRICK VENEERS SHALL BE ATTACHED TO FRAMING WITH MINIMUM 22 GAUGE GALVANIZED CORRUGATED STEEL TIIES 7/8" WIDE 16" O.C VERTICALLY AND 32" O.C HORIZONTALLY.

3) WEEP HOLES SHALL BE WITHIN THE FIRST COURSE ABOVE GRADE AND WITHIN THE FIRST COURSDE ABOVE STEEL LINTELS. WEEP HOLES SHALL NOT BE LESS THAN 3/16" DIAMETER AND NO MORE THAN 33" O.C.

4) VENEER FLASHING SHALL BE IN ACCORDANCE WITH IRC R703.8.5

5) ALL MASONRY FOUNDATION CONSTRUCTION SHALL BE INSTALLED IN ACCORDANCE WITH TMS 402, ACI 530, ASCE 5 NCMA TR86-A. THE IRC PRESCRIPTIVE CODE MAY BE USED AS AN ALTERNATIVE.

Sheet List

Sheet Number	Sheet Name
S.01	COVER
S.02	FLOOR FRAMING PLAN
S.03	FOUNDATION PLAN
S.04	ROOF FRAMING PLAN
S.05	SECTIONS

1632


Project Name

Project Address

Home Addition

6107 Bay St, Richmond VA 23226

8/1/2025 7:53:57 PM

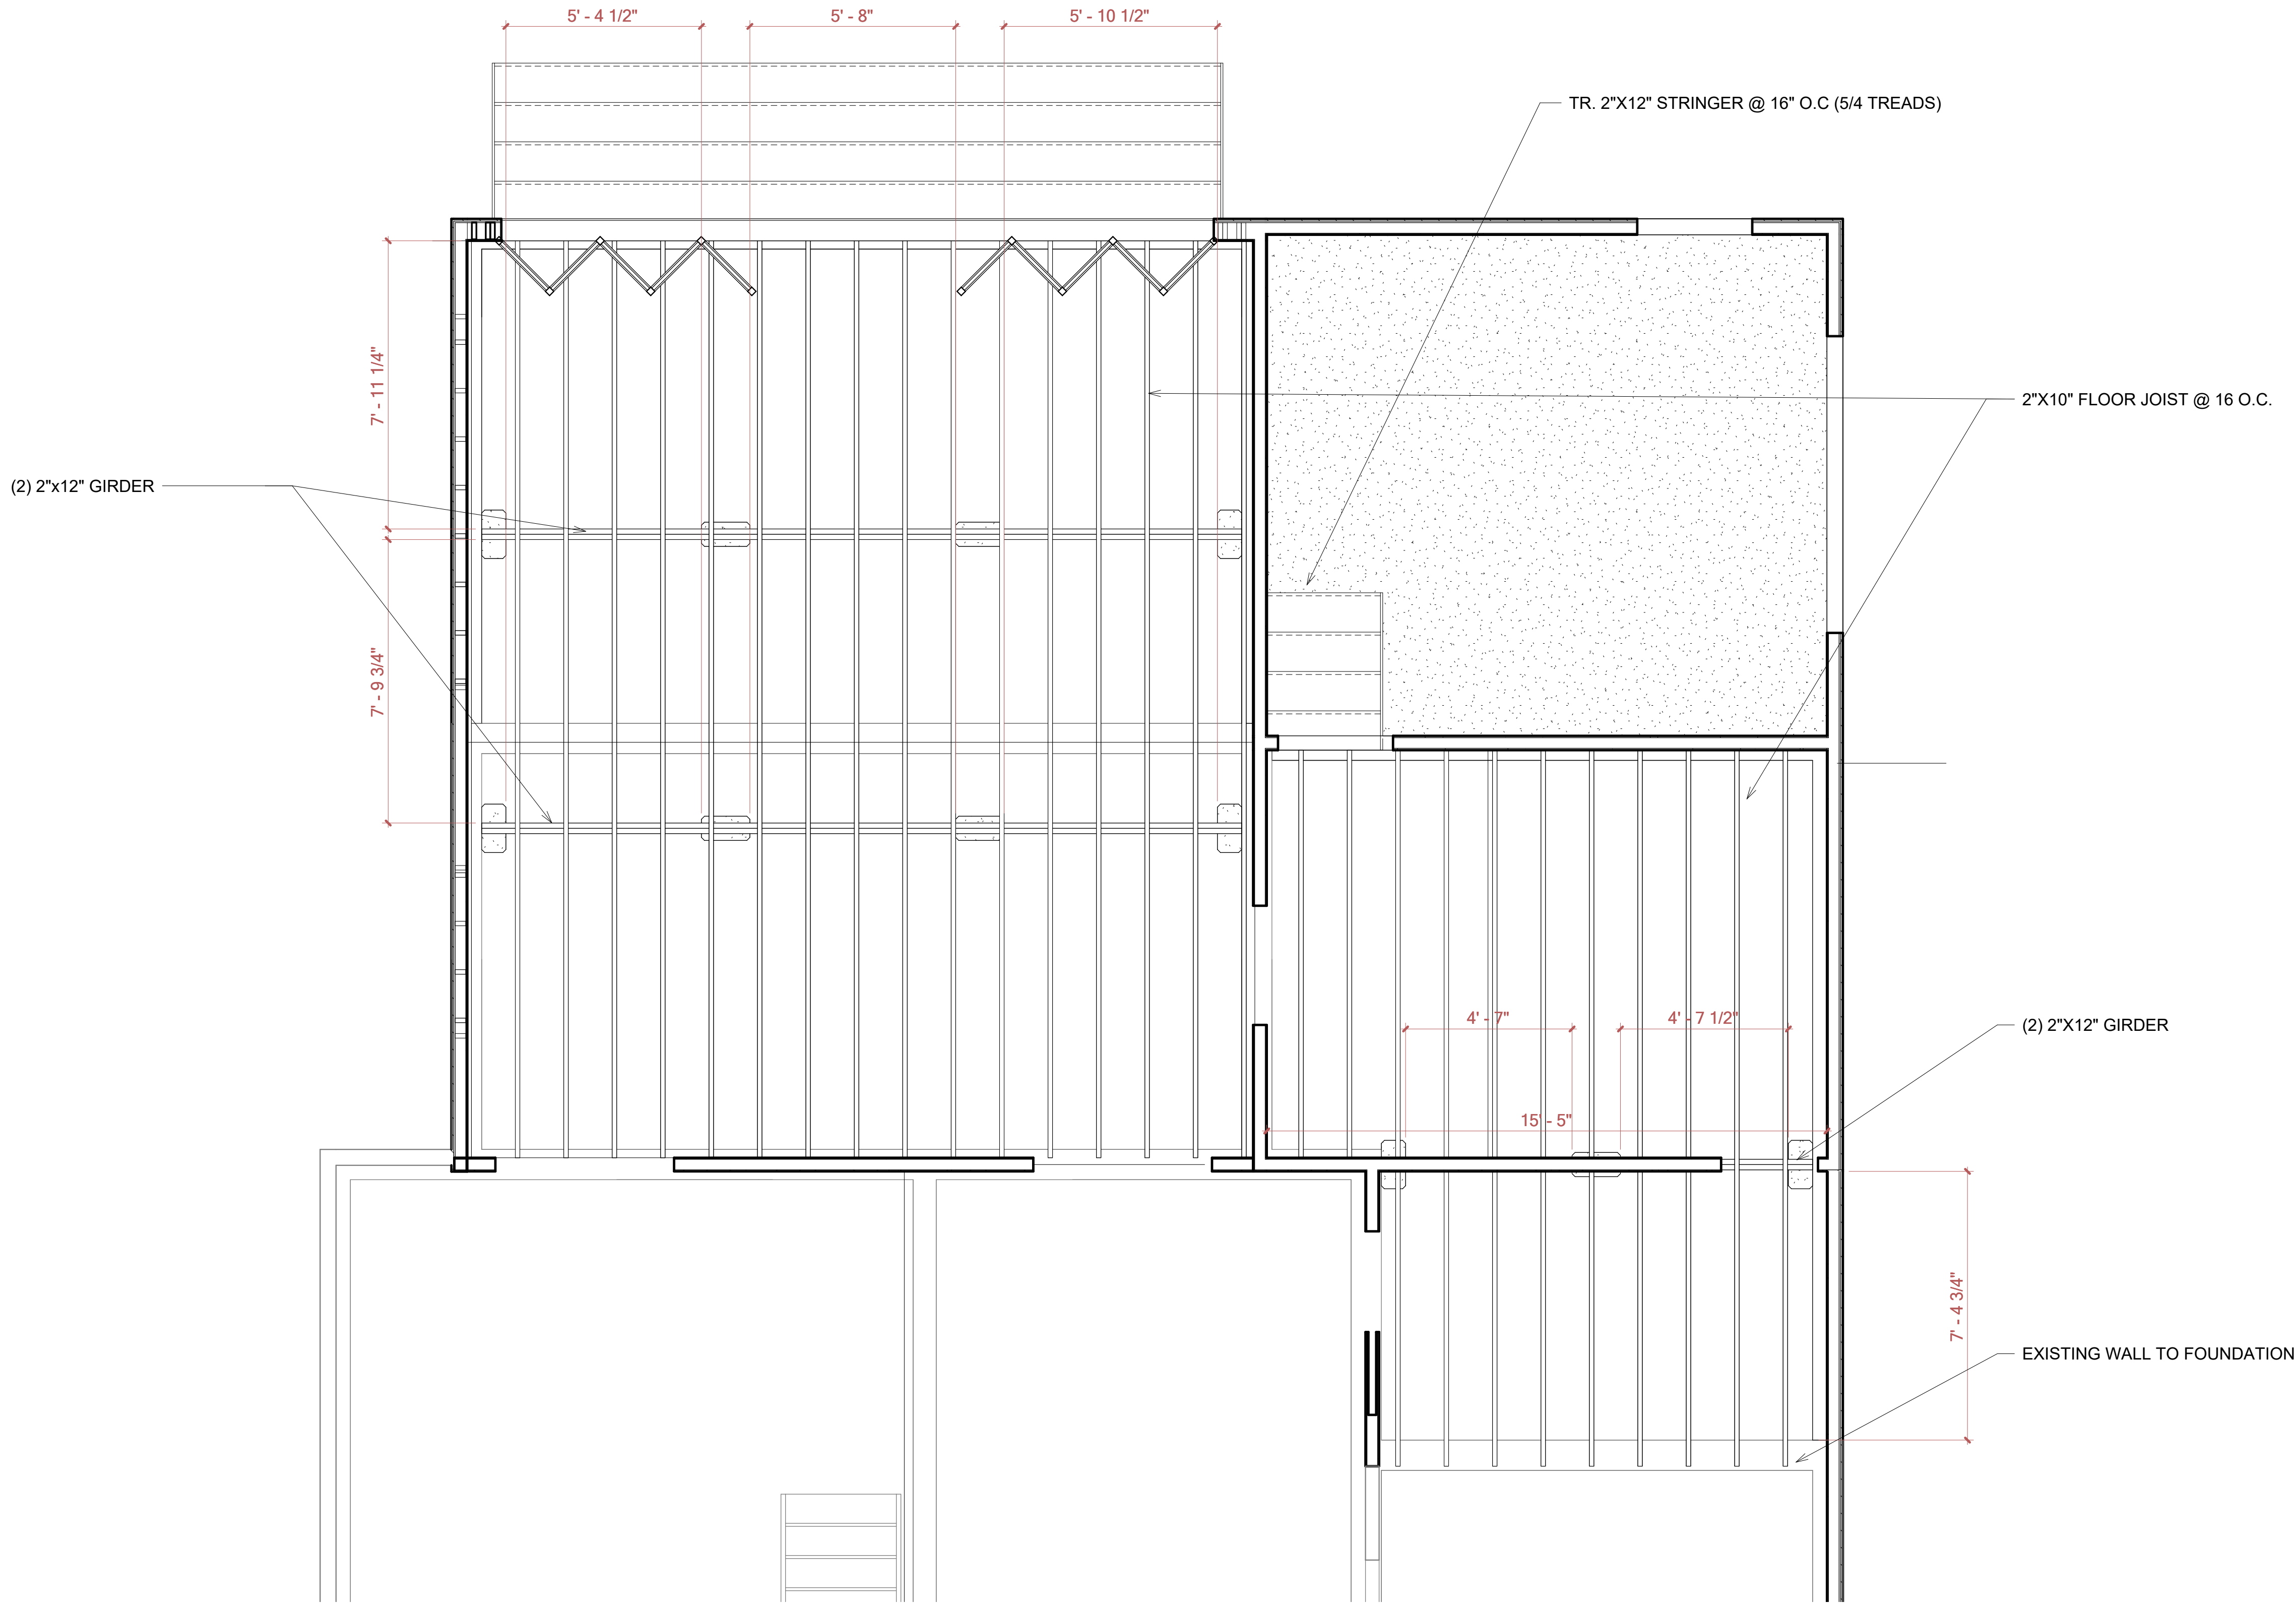

1 S.F.P - FLOOR FRAMING PLAN
3/8" = 1'-0"

16 32

Phone
Office Address


FLOOR
FRAMING
PLAN

Notes


Rev Num.	Description	Date

Project Name	Project Status	Date	Scale	Sheet Num.
Home Addition	Planning and Permits	07/09/02	3/8" = 1'-0"	S.02
Project Adress	Proyect Number	Current Revision	North	File Path
6107 Bay St, Richmond VA 23226	001		↑	C:\Users\gerso\Downloads\6107 Bay St Richmond -- structural -- correction-7-28-25.rvt


e-mail

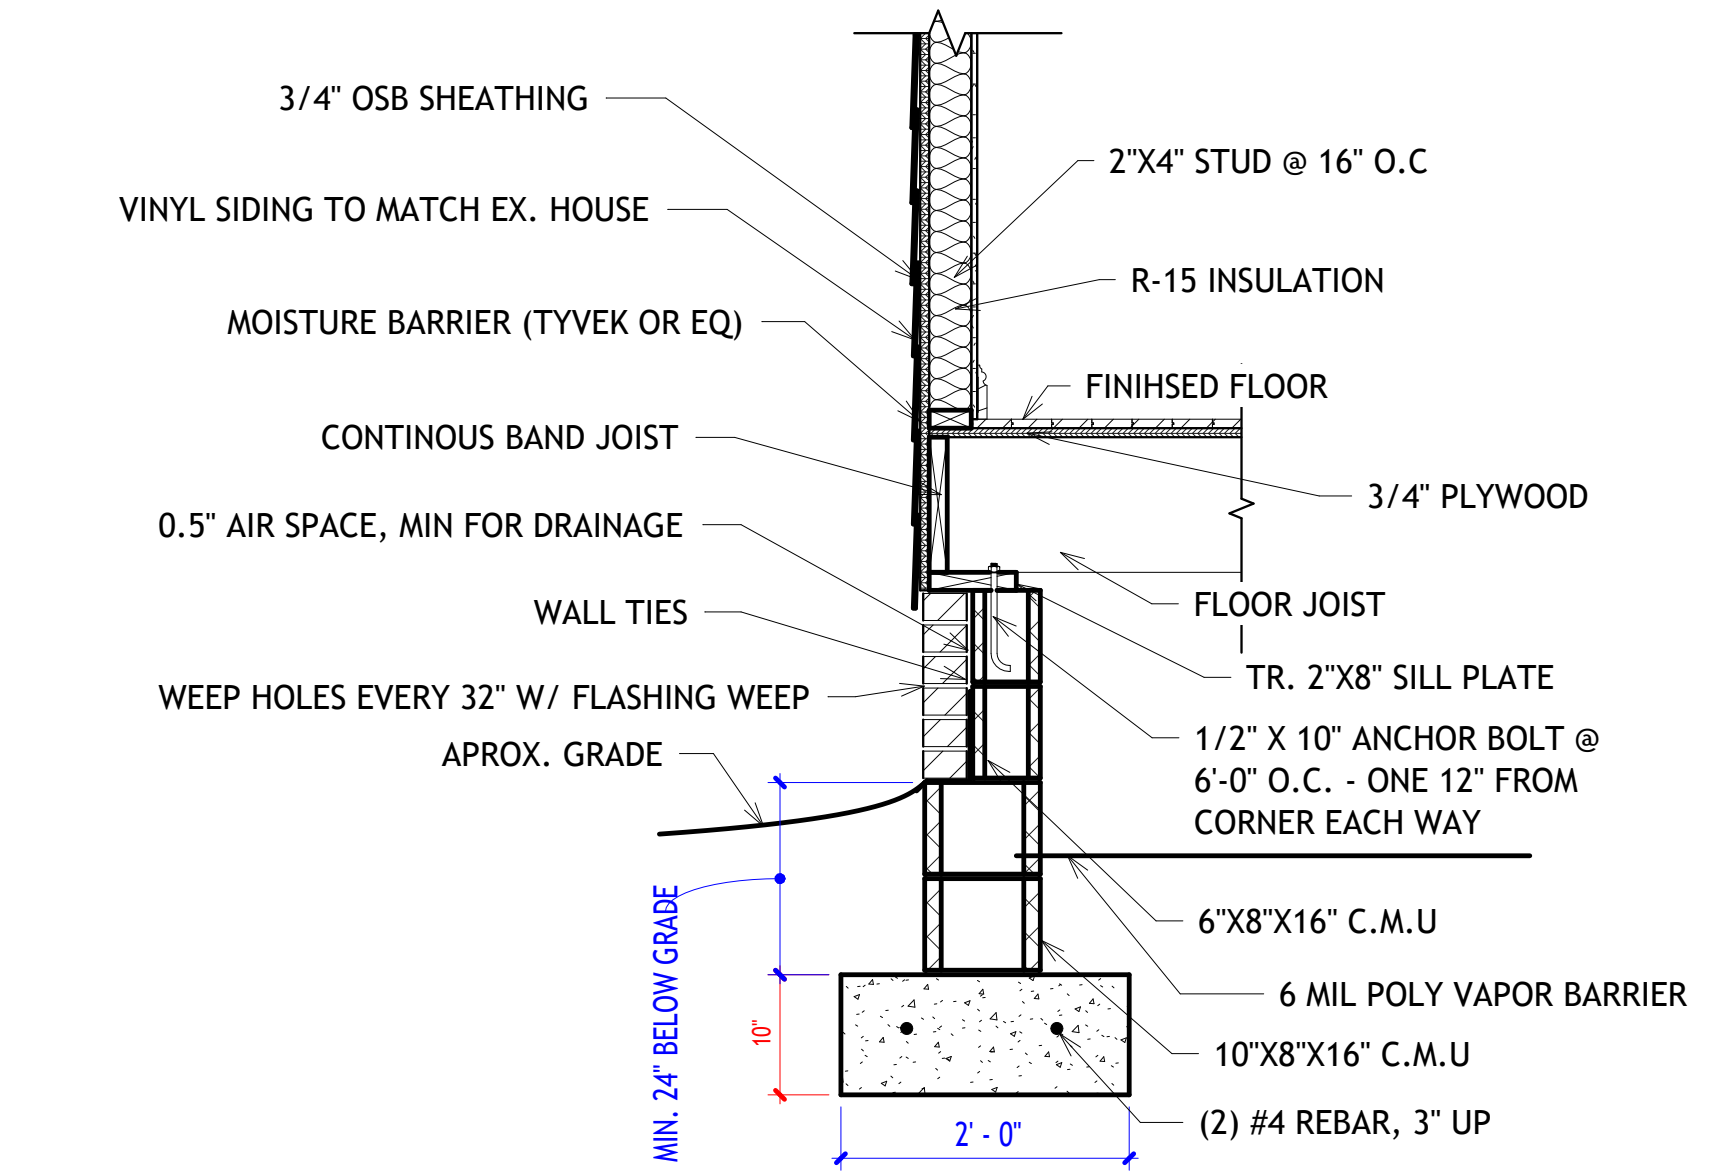


2 FOUNDATION DETAIL
3/4" = 1'-0"

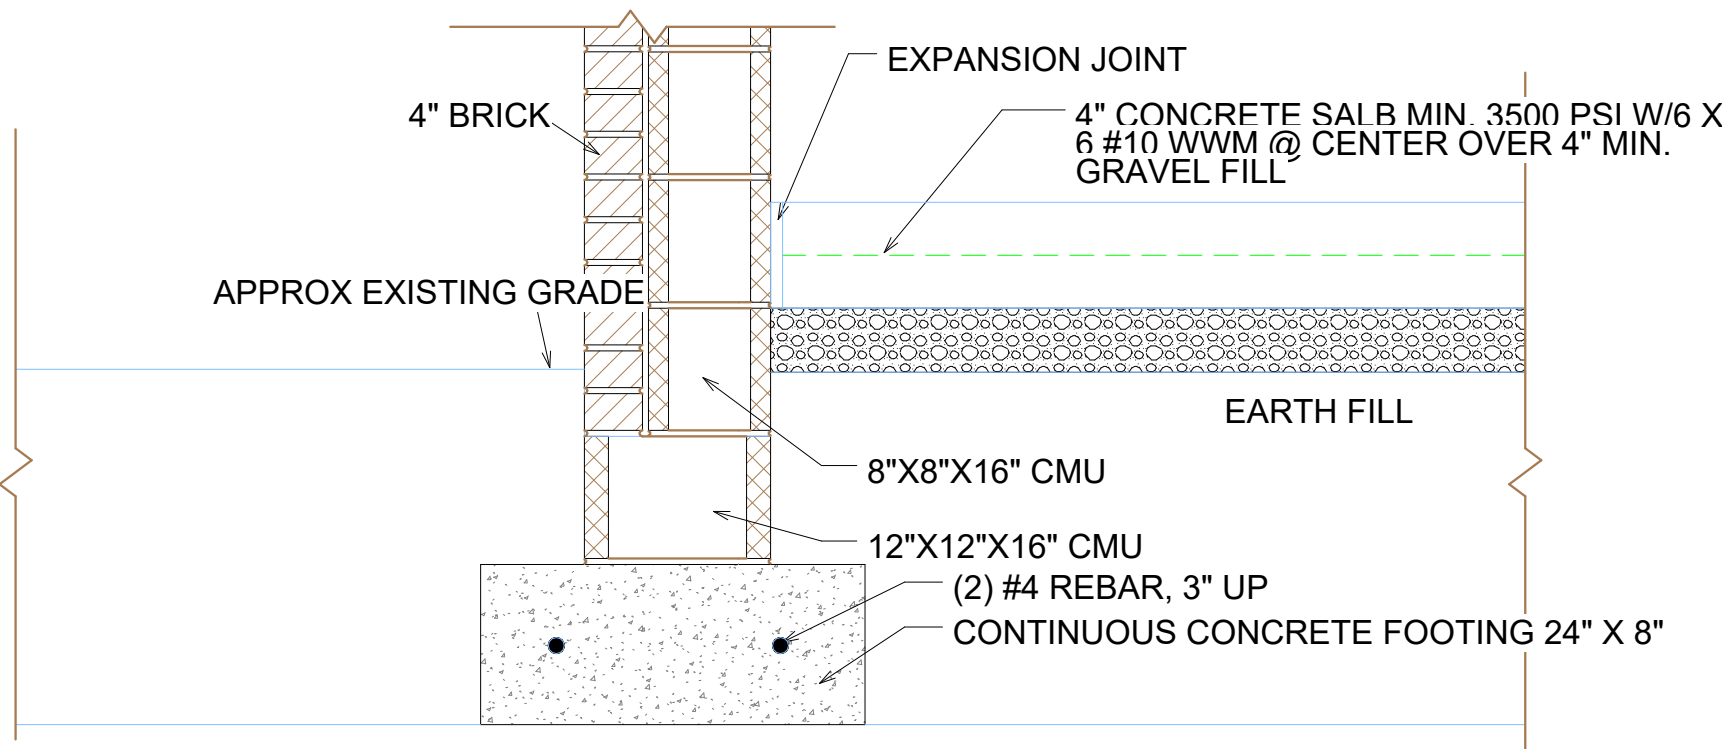

3 GARAGE FLOOR SECTION
1" = 1'-0"

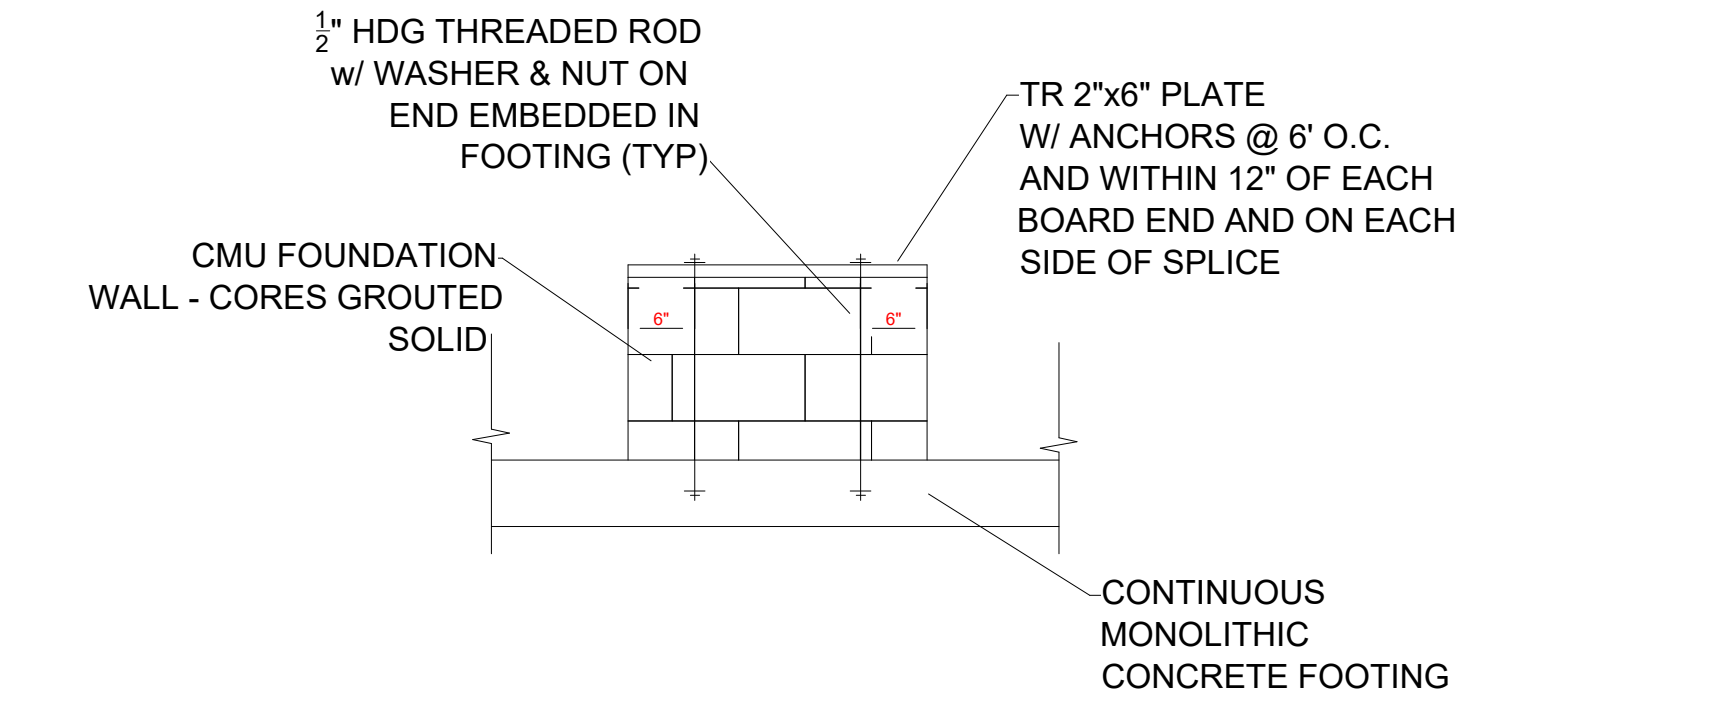


4 STEM WALL DETAIL
12" = 1'-0"

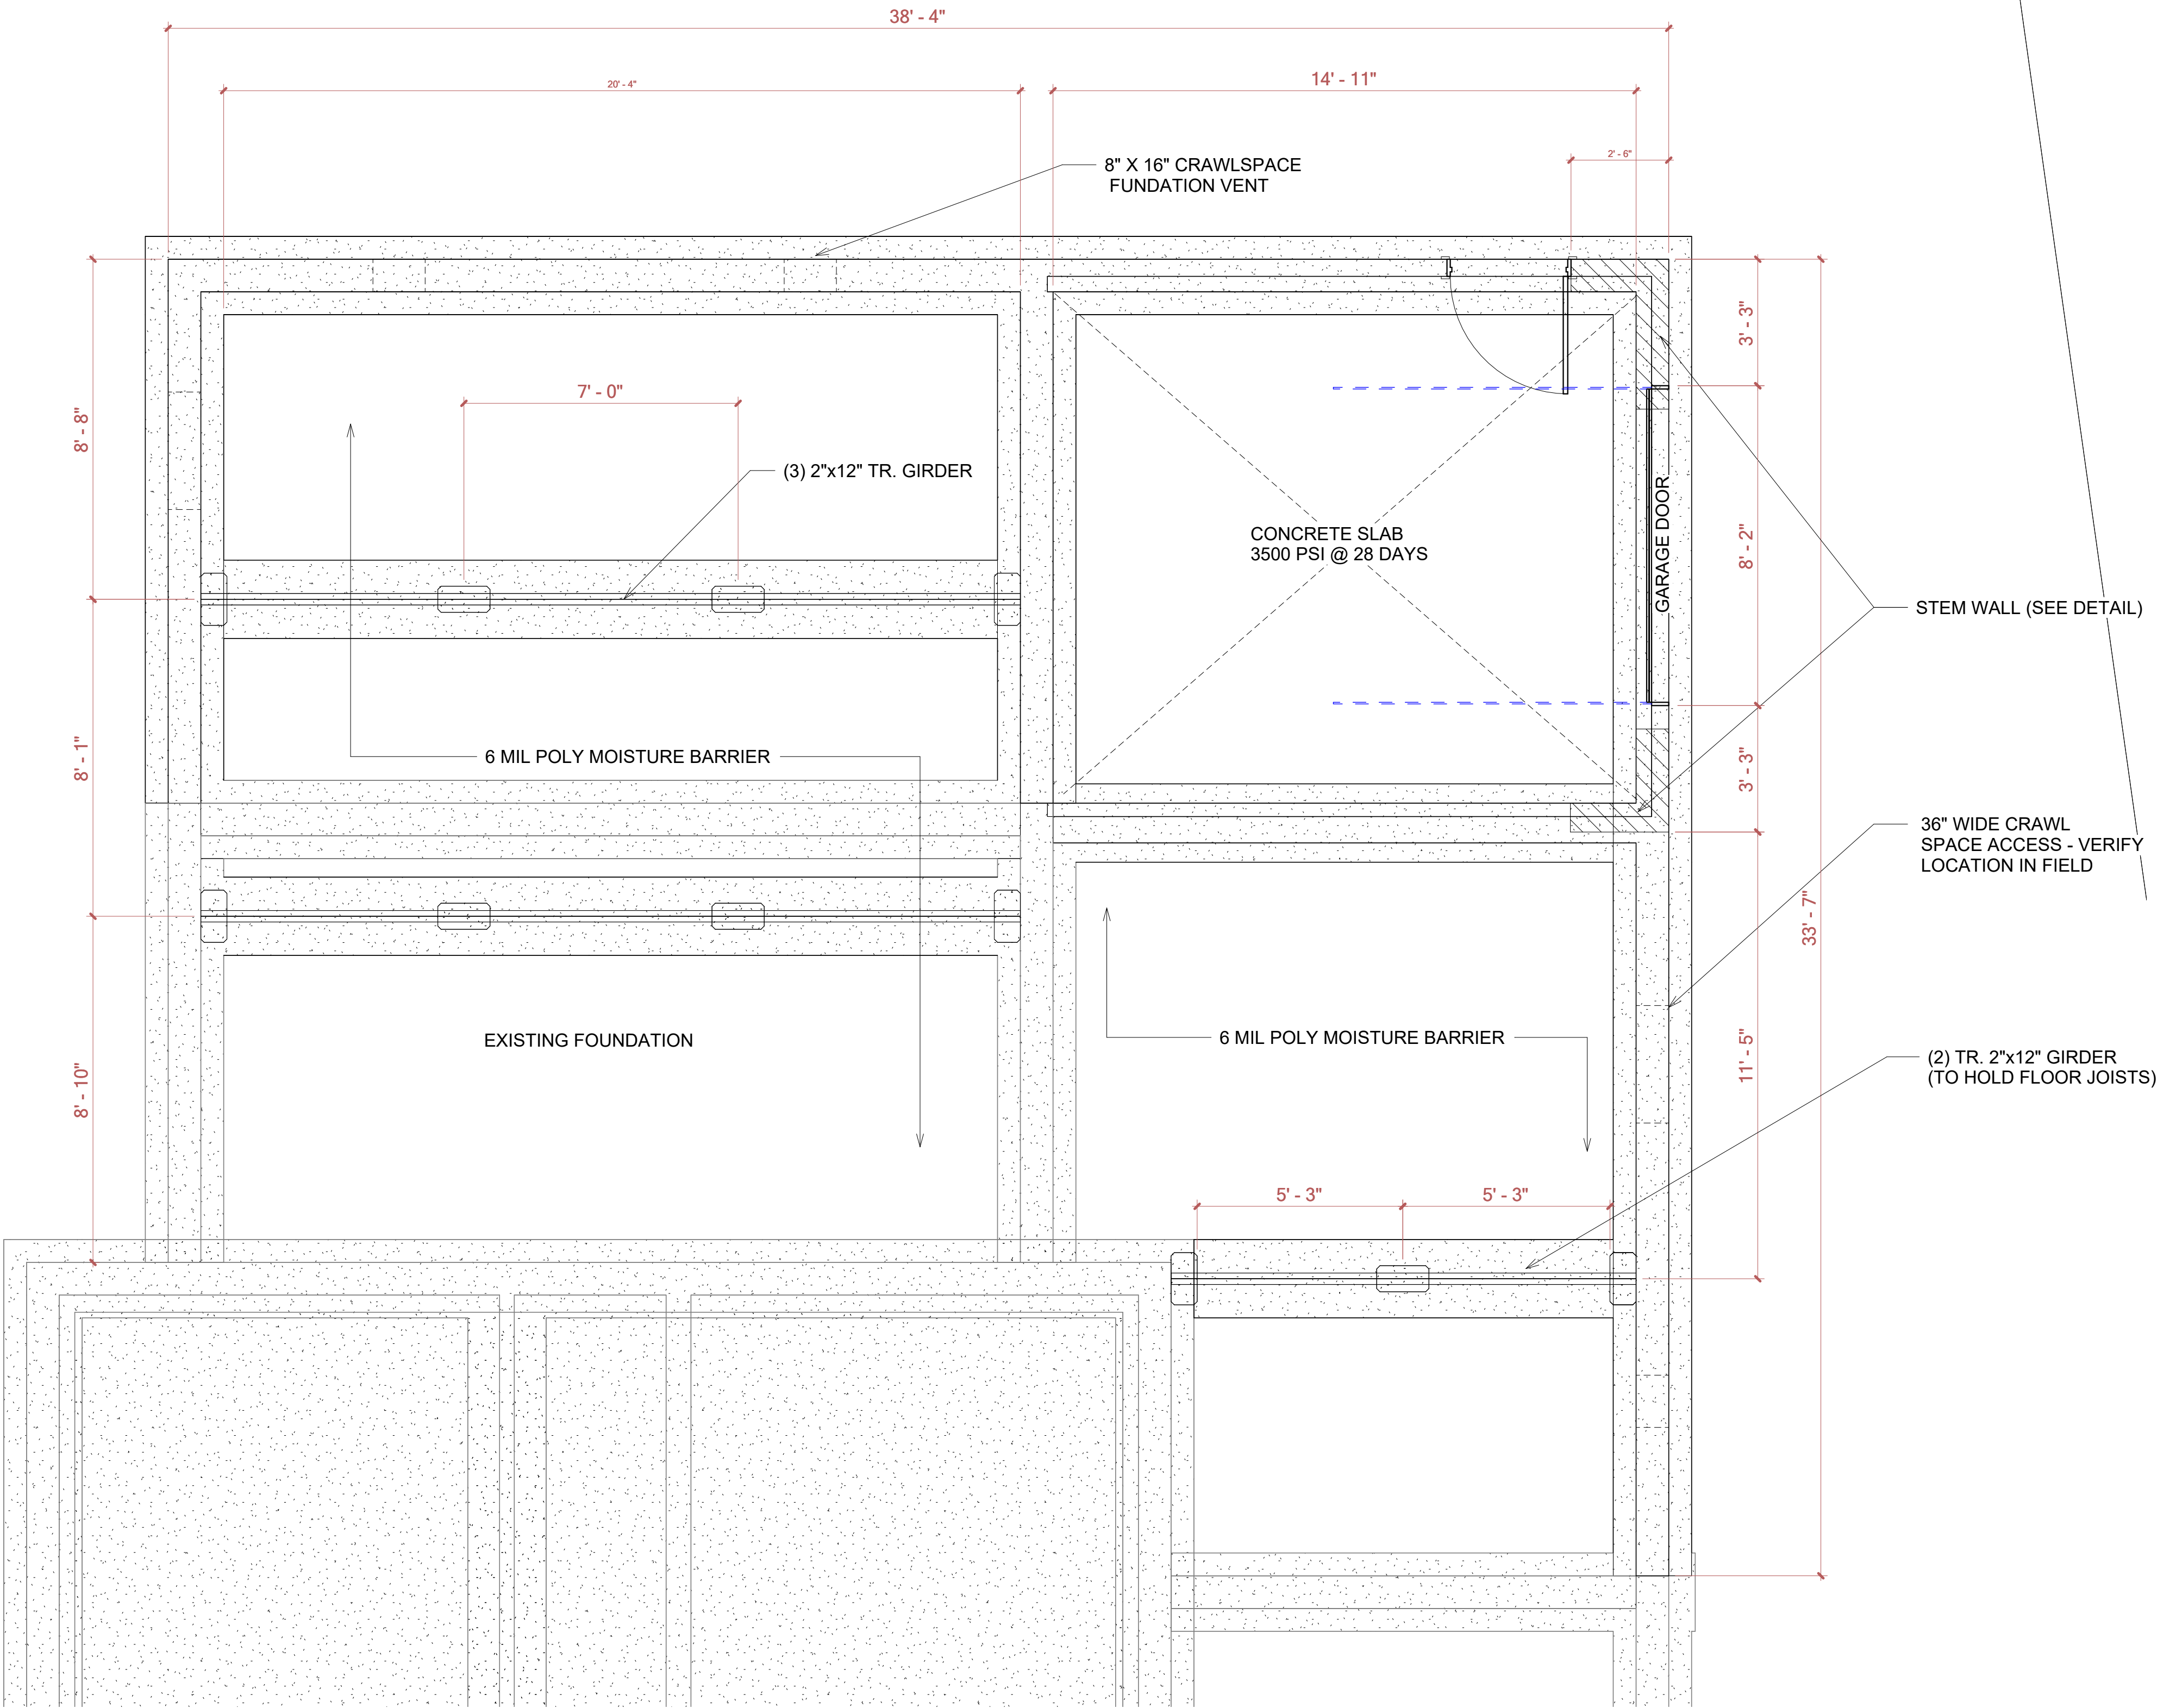


1 S.F.P. FOUNDATION PLAN
3/8" = 1'-0"

1632	Phone	FOUNDATION PLAN	Notes	<table><tr><th>Rev Num.</th><th>Description</th><th>Date</th></tr><tr><td></td><td></td><td></td></tr><tr><td></td><td></td><td></td></tr><tr><td></td><td></td><td></td></tr><tr><td></td><td></td><td></td></tr></table>	Rev Num.	Description	Date													Project Name	Project Status	Date	Scale	Sheet Num.
	Rev Num.				Description	Date																		
Office Address			Home Addition	Planning and Permits	07/09/02	As indicated	S.03																	
			Project Adress	Proyect Number	Current Revision	North	File Path																	
			6107 Bay St, Richmond VA 23226	001		↑	C:\Users\gerso\Downloads\6107 Bay St Richmond -- structural -- correction-7-28-25.rvt																	
e-mail																								

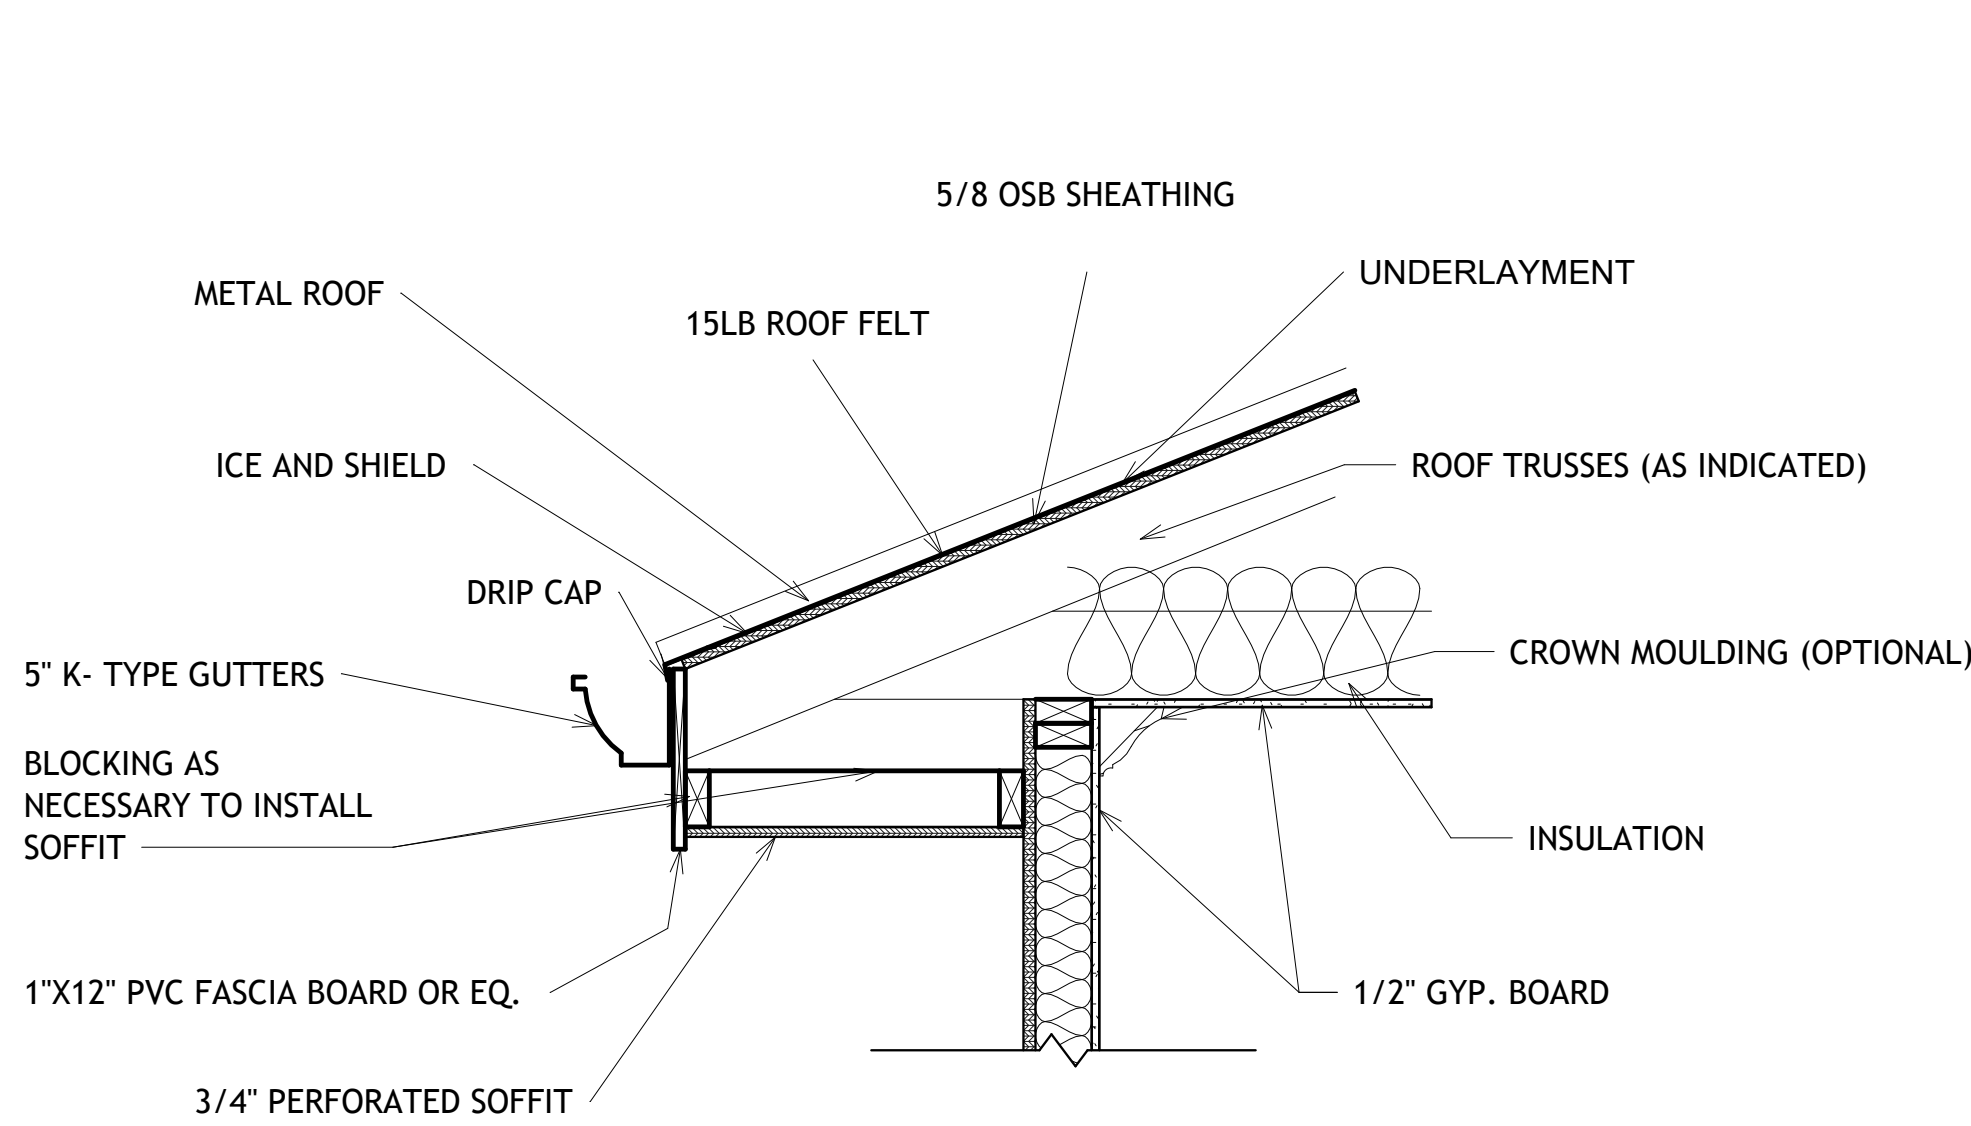

2 TYP SOFFIT DETAIL
1" = 1'-0"

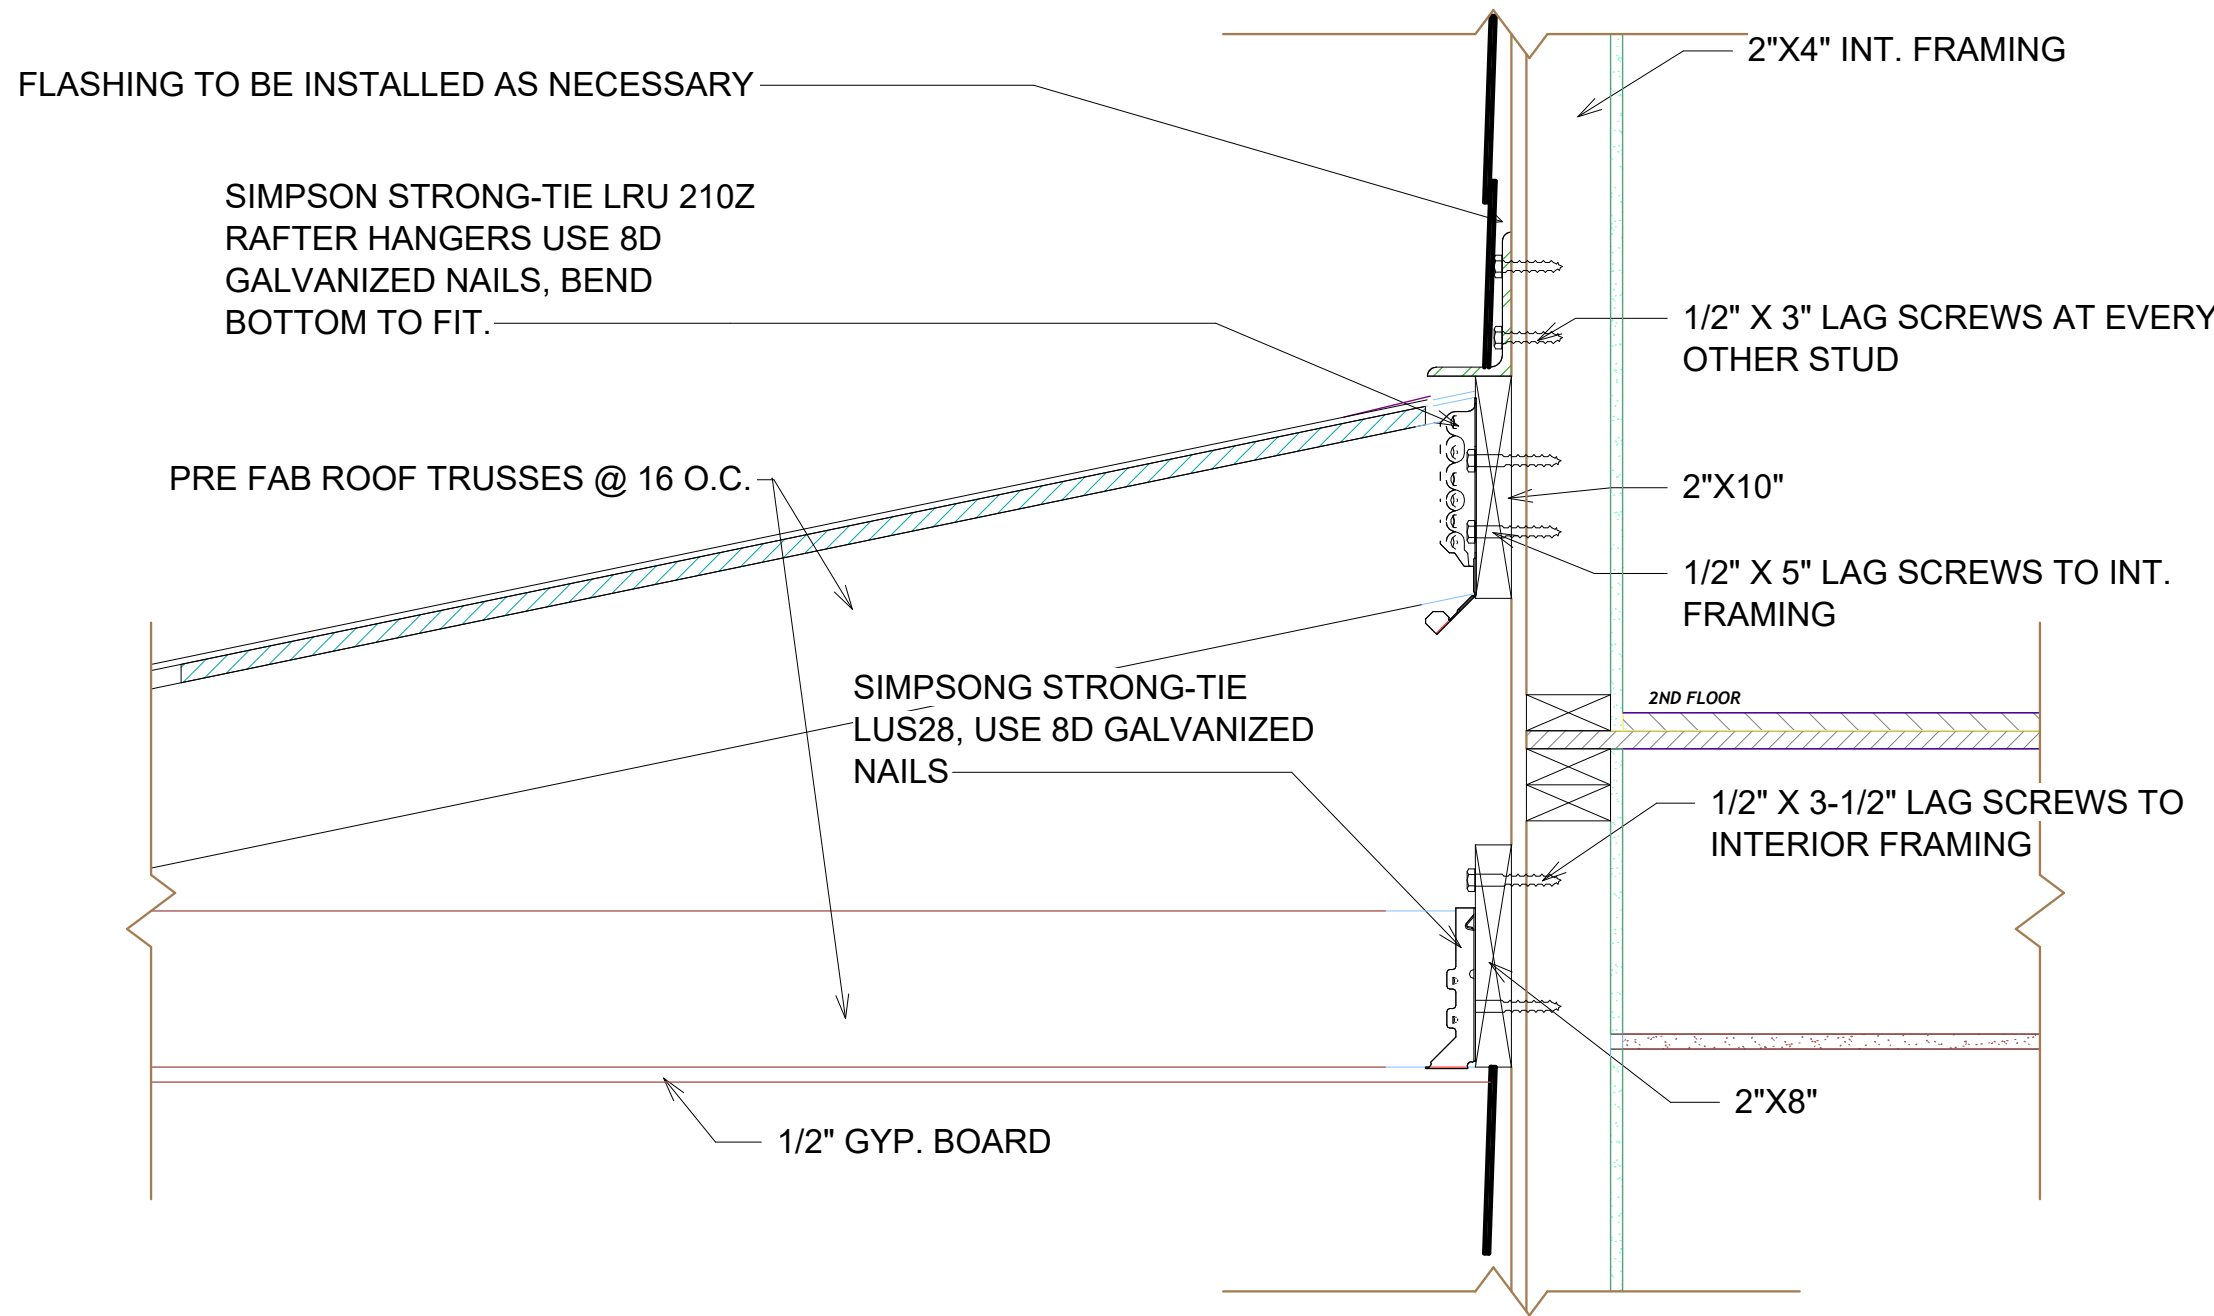

3 ATTACHMENT TO WALL DETAIL
1 1/2" = 1'-0"



1 ROOF PLAN
1/4" = 1'-0"

1632


Phone
Office Address

ROOF
FRAMING
PLAN


Notes

Rev Num.	Description	Date


Project Name	Project Status	Date	Scale	Sheet Num.
Home Addition	Planning and Permits	07/09/02	As indicated	S.04
Project Address	Proyect Number	Current Revision	North	File Path
6107 Bay St, Richmond VA 23226	001		↑	C:\Users\gerso\Downloads\6107 Bay St Richmond -- structural -- correction-7-28-25.rvt

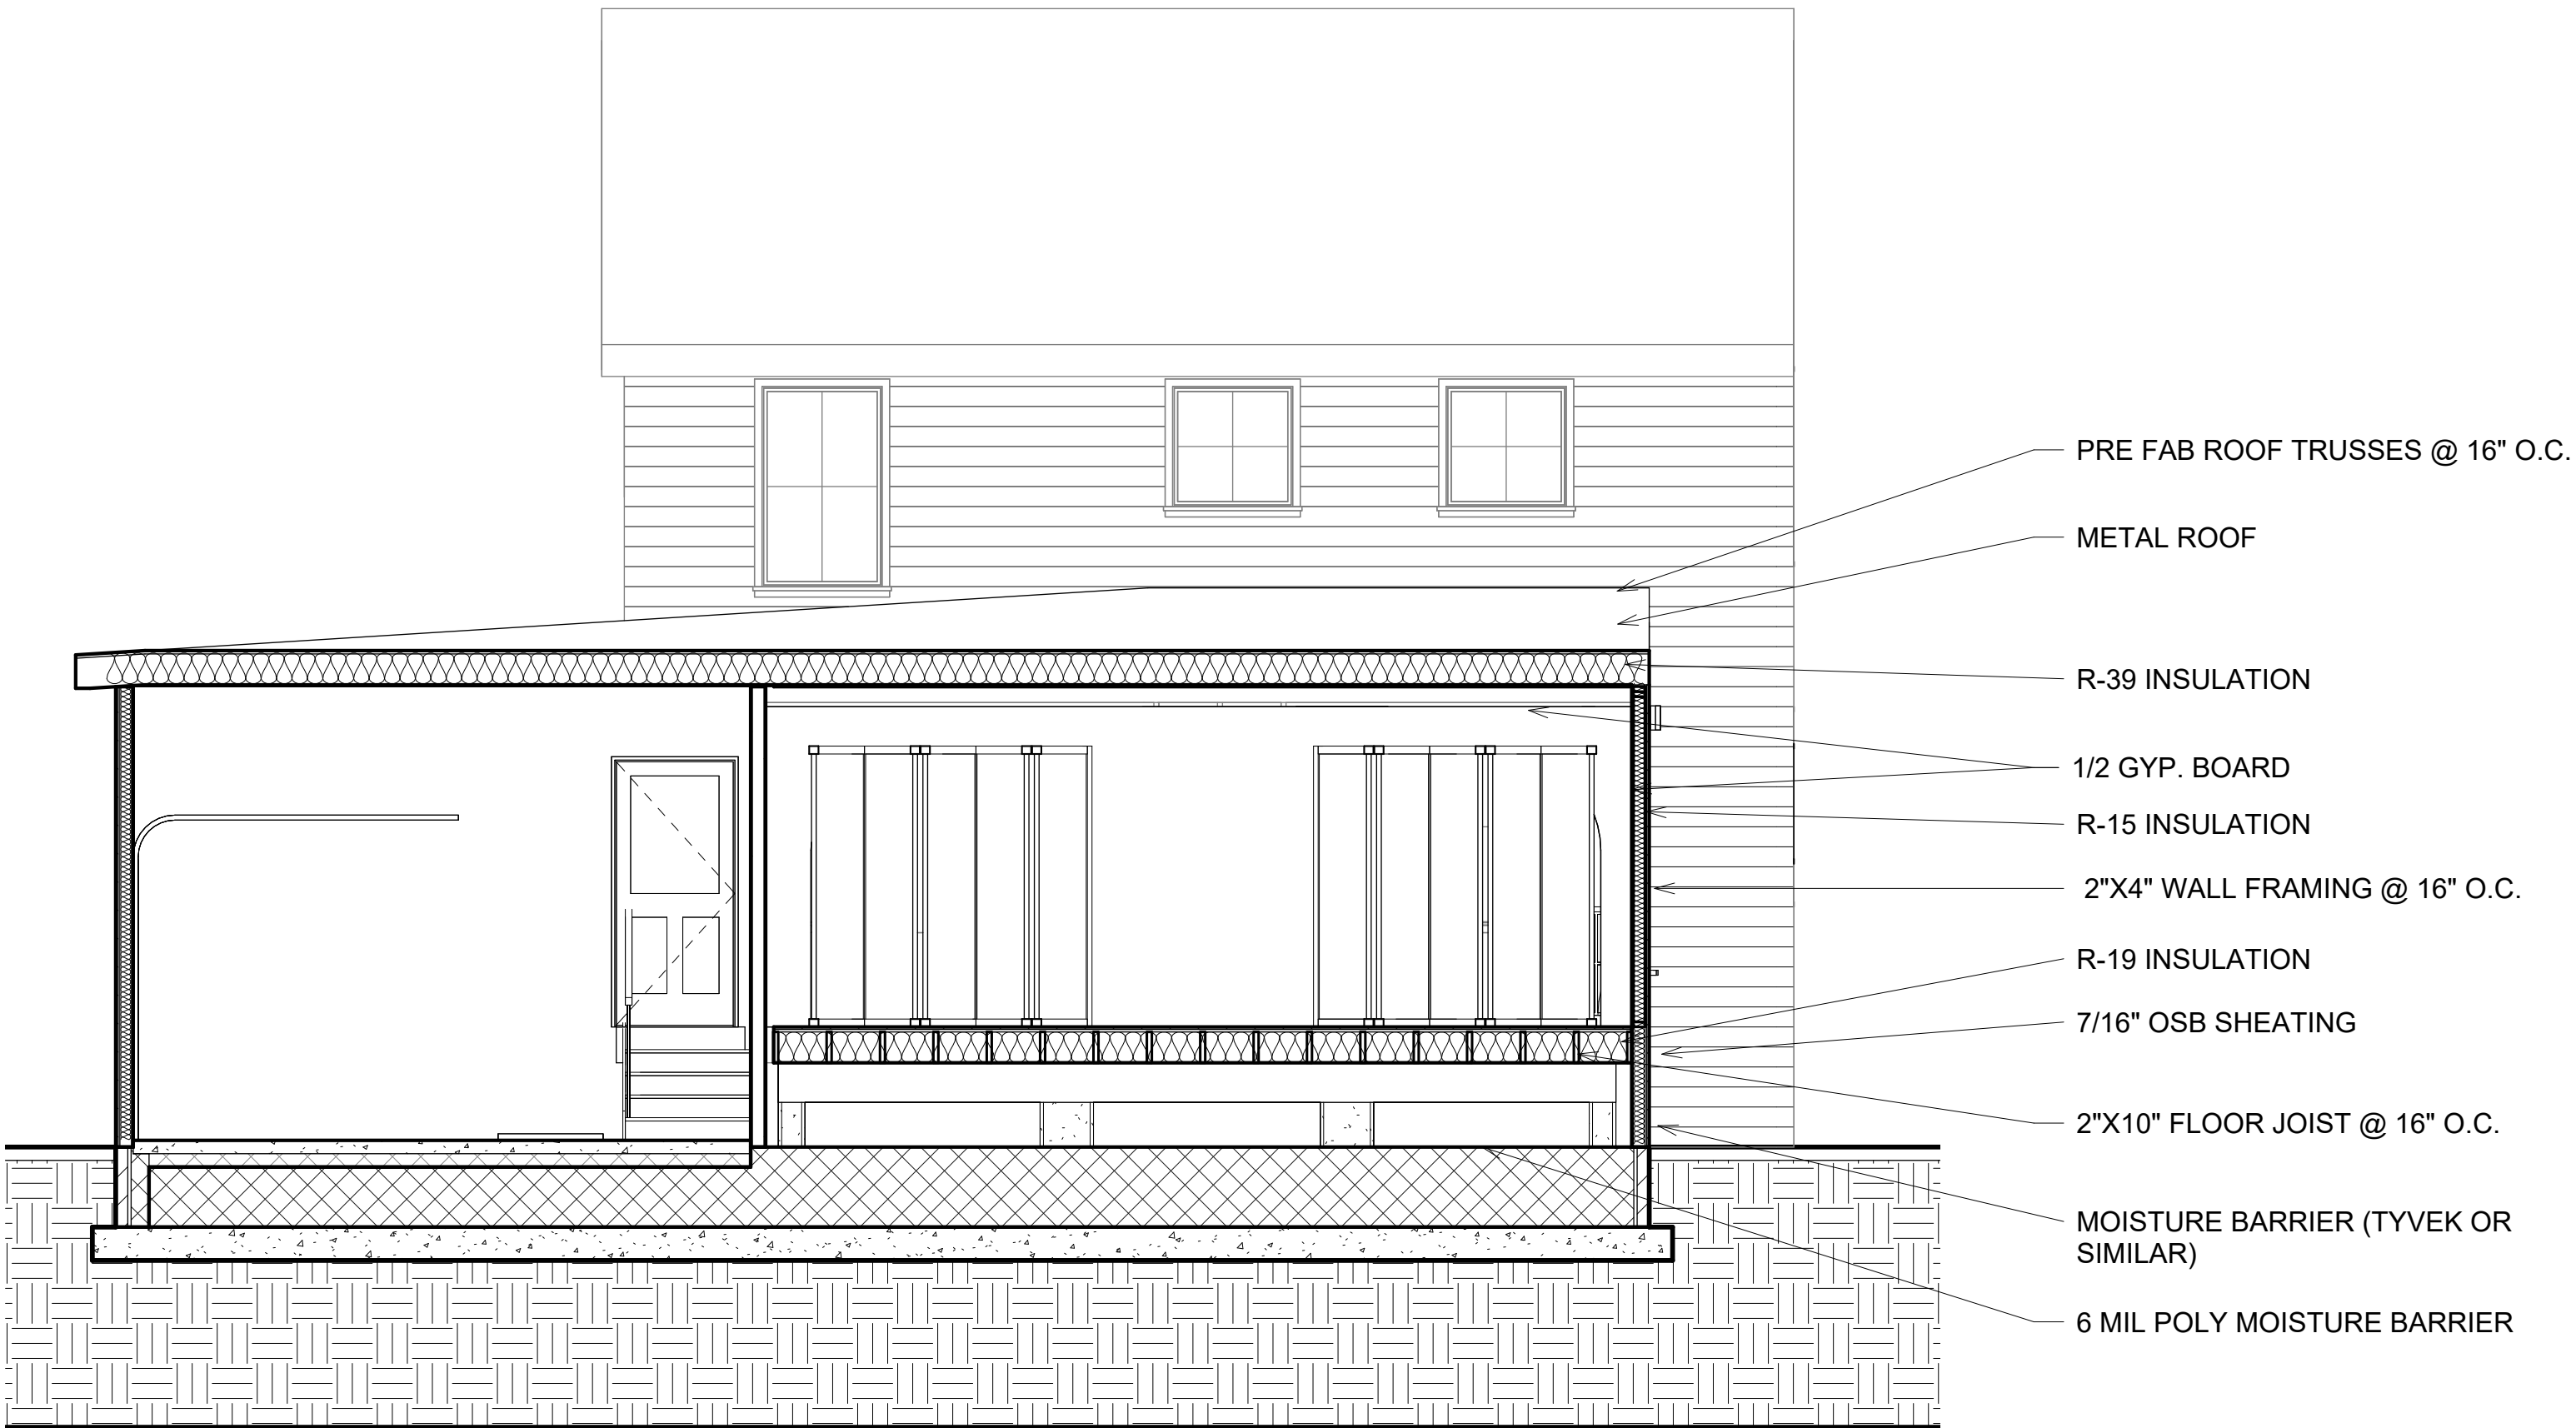


1 Section 1
1/4" = 1'-0"

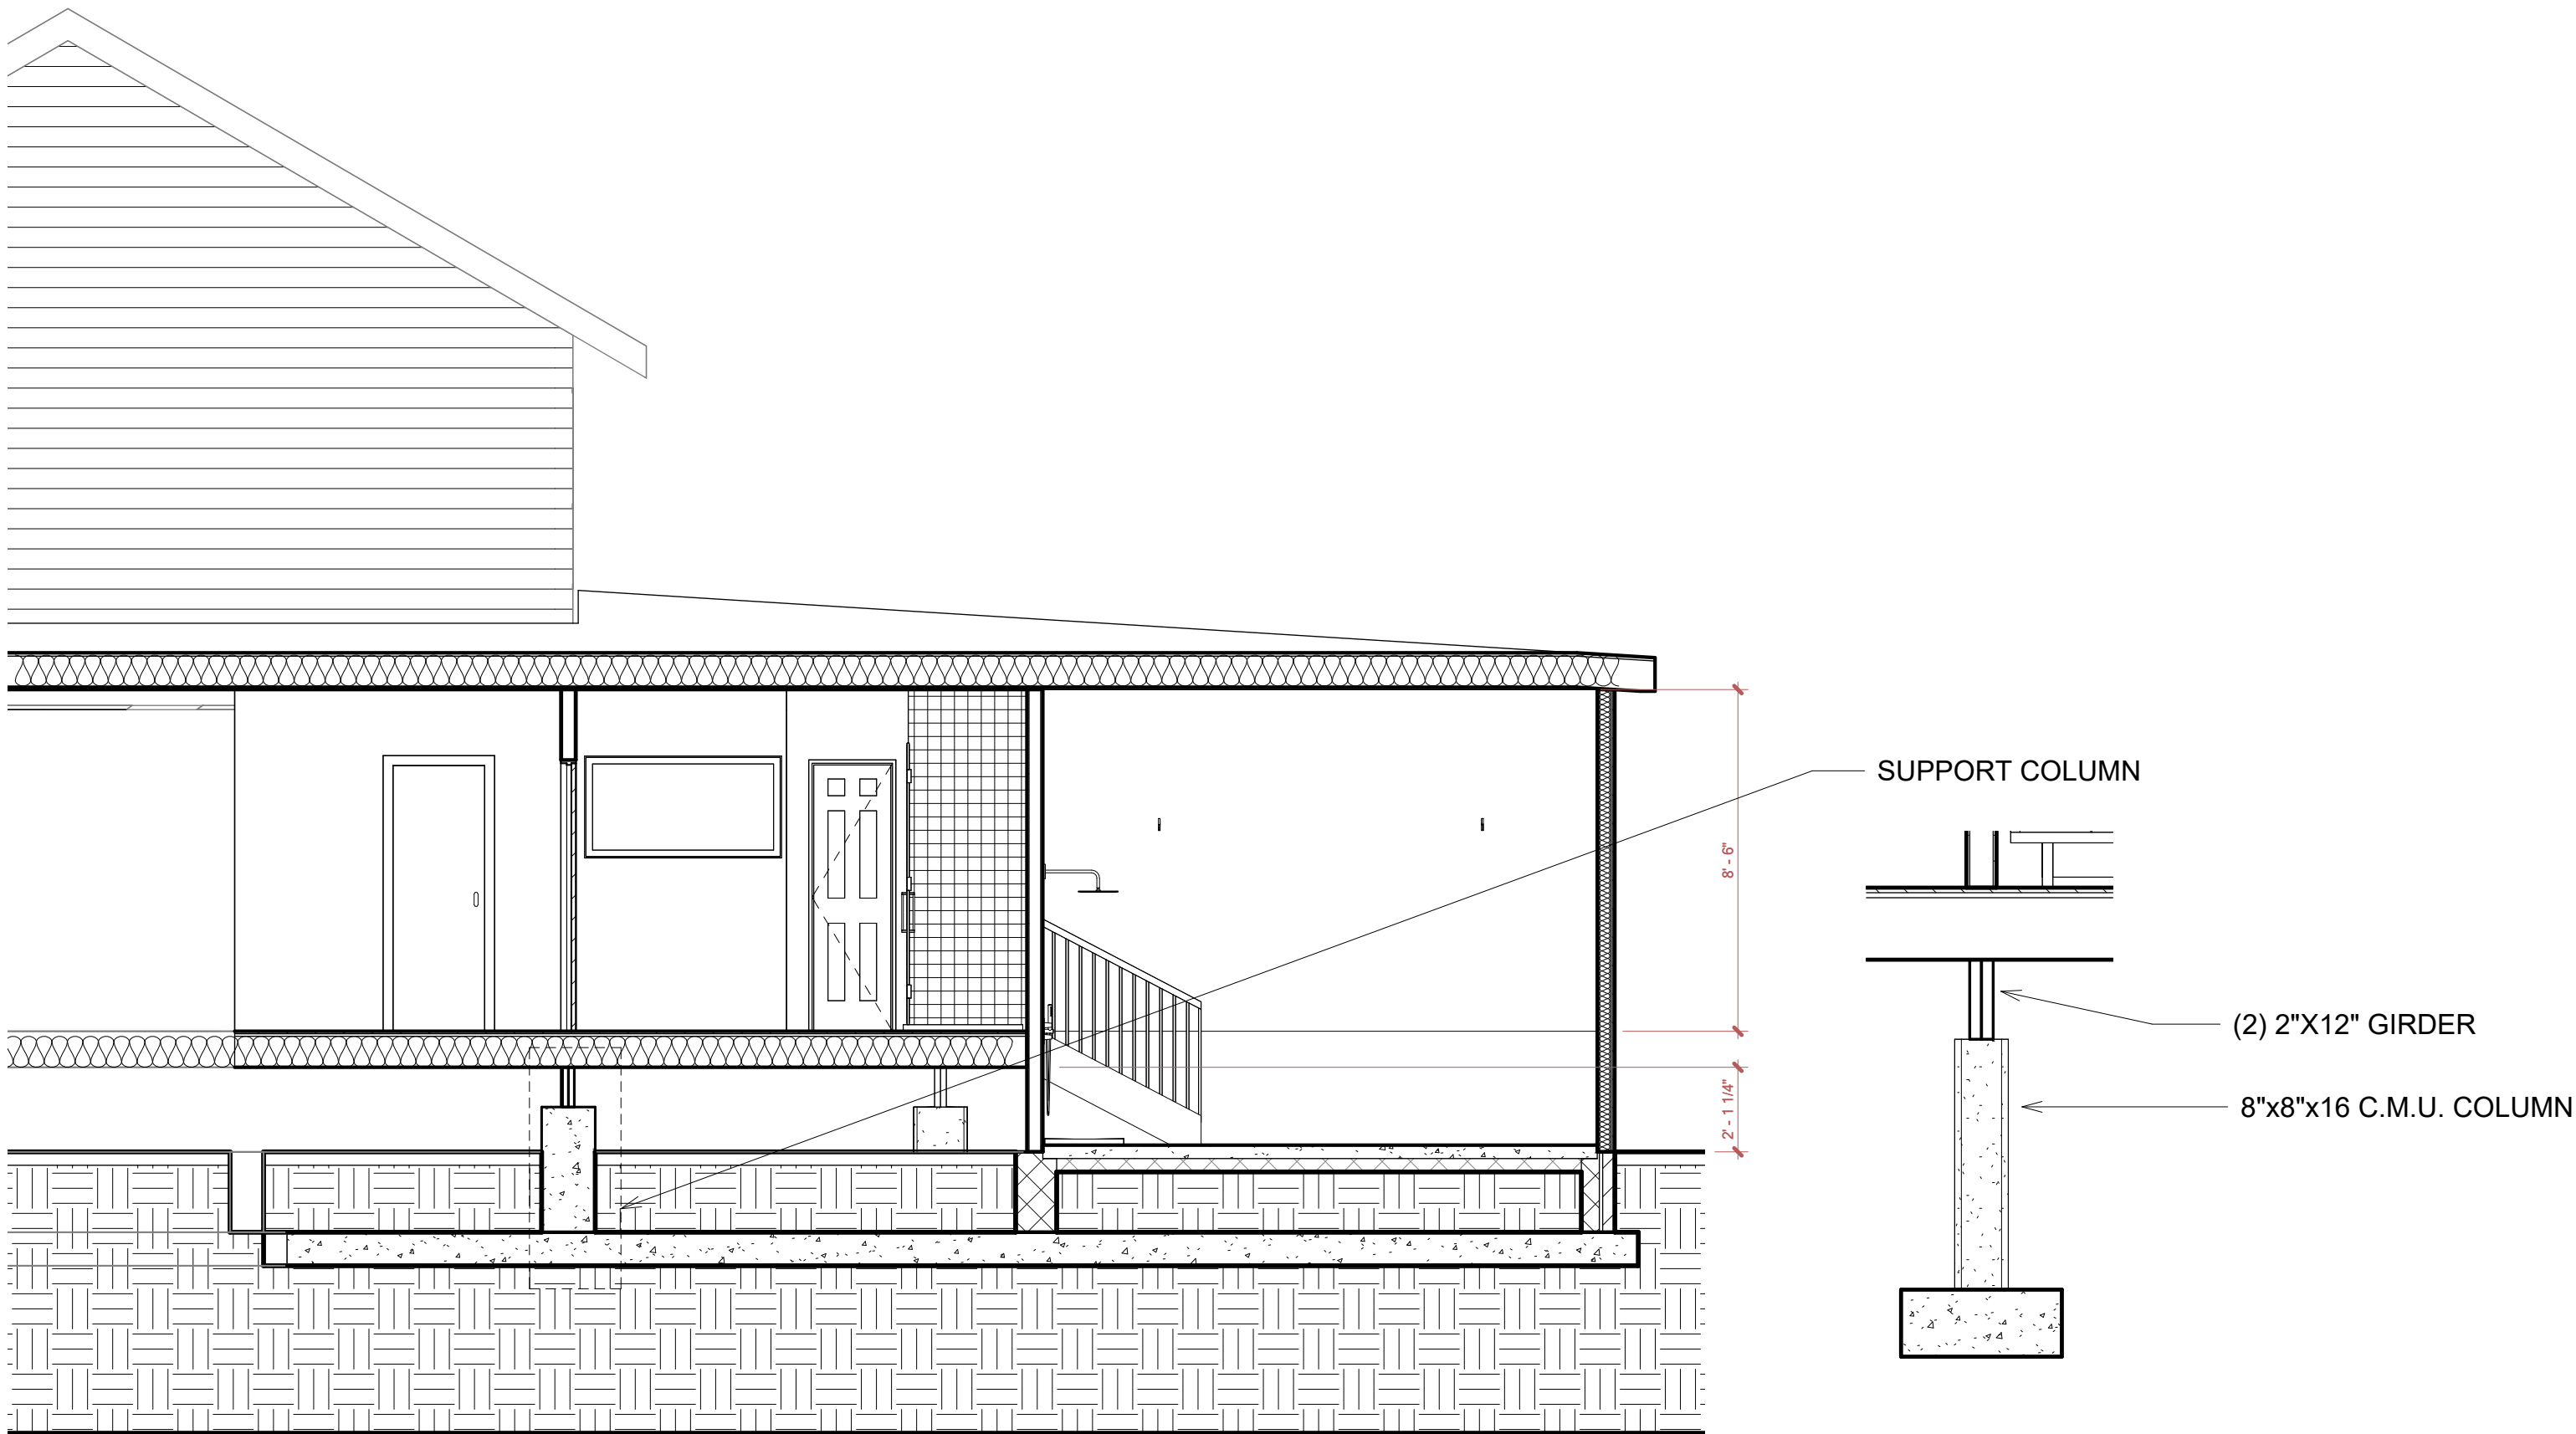

2 Section 2
1/4" = 1'-0"

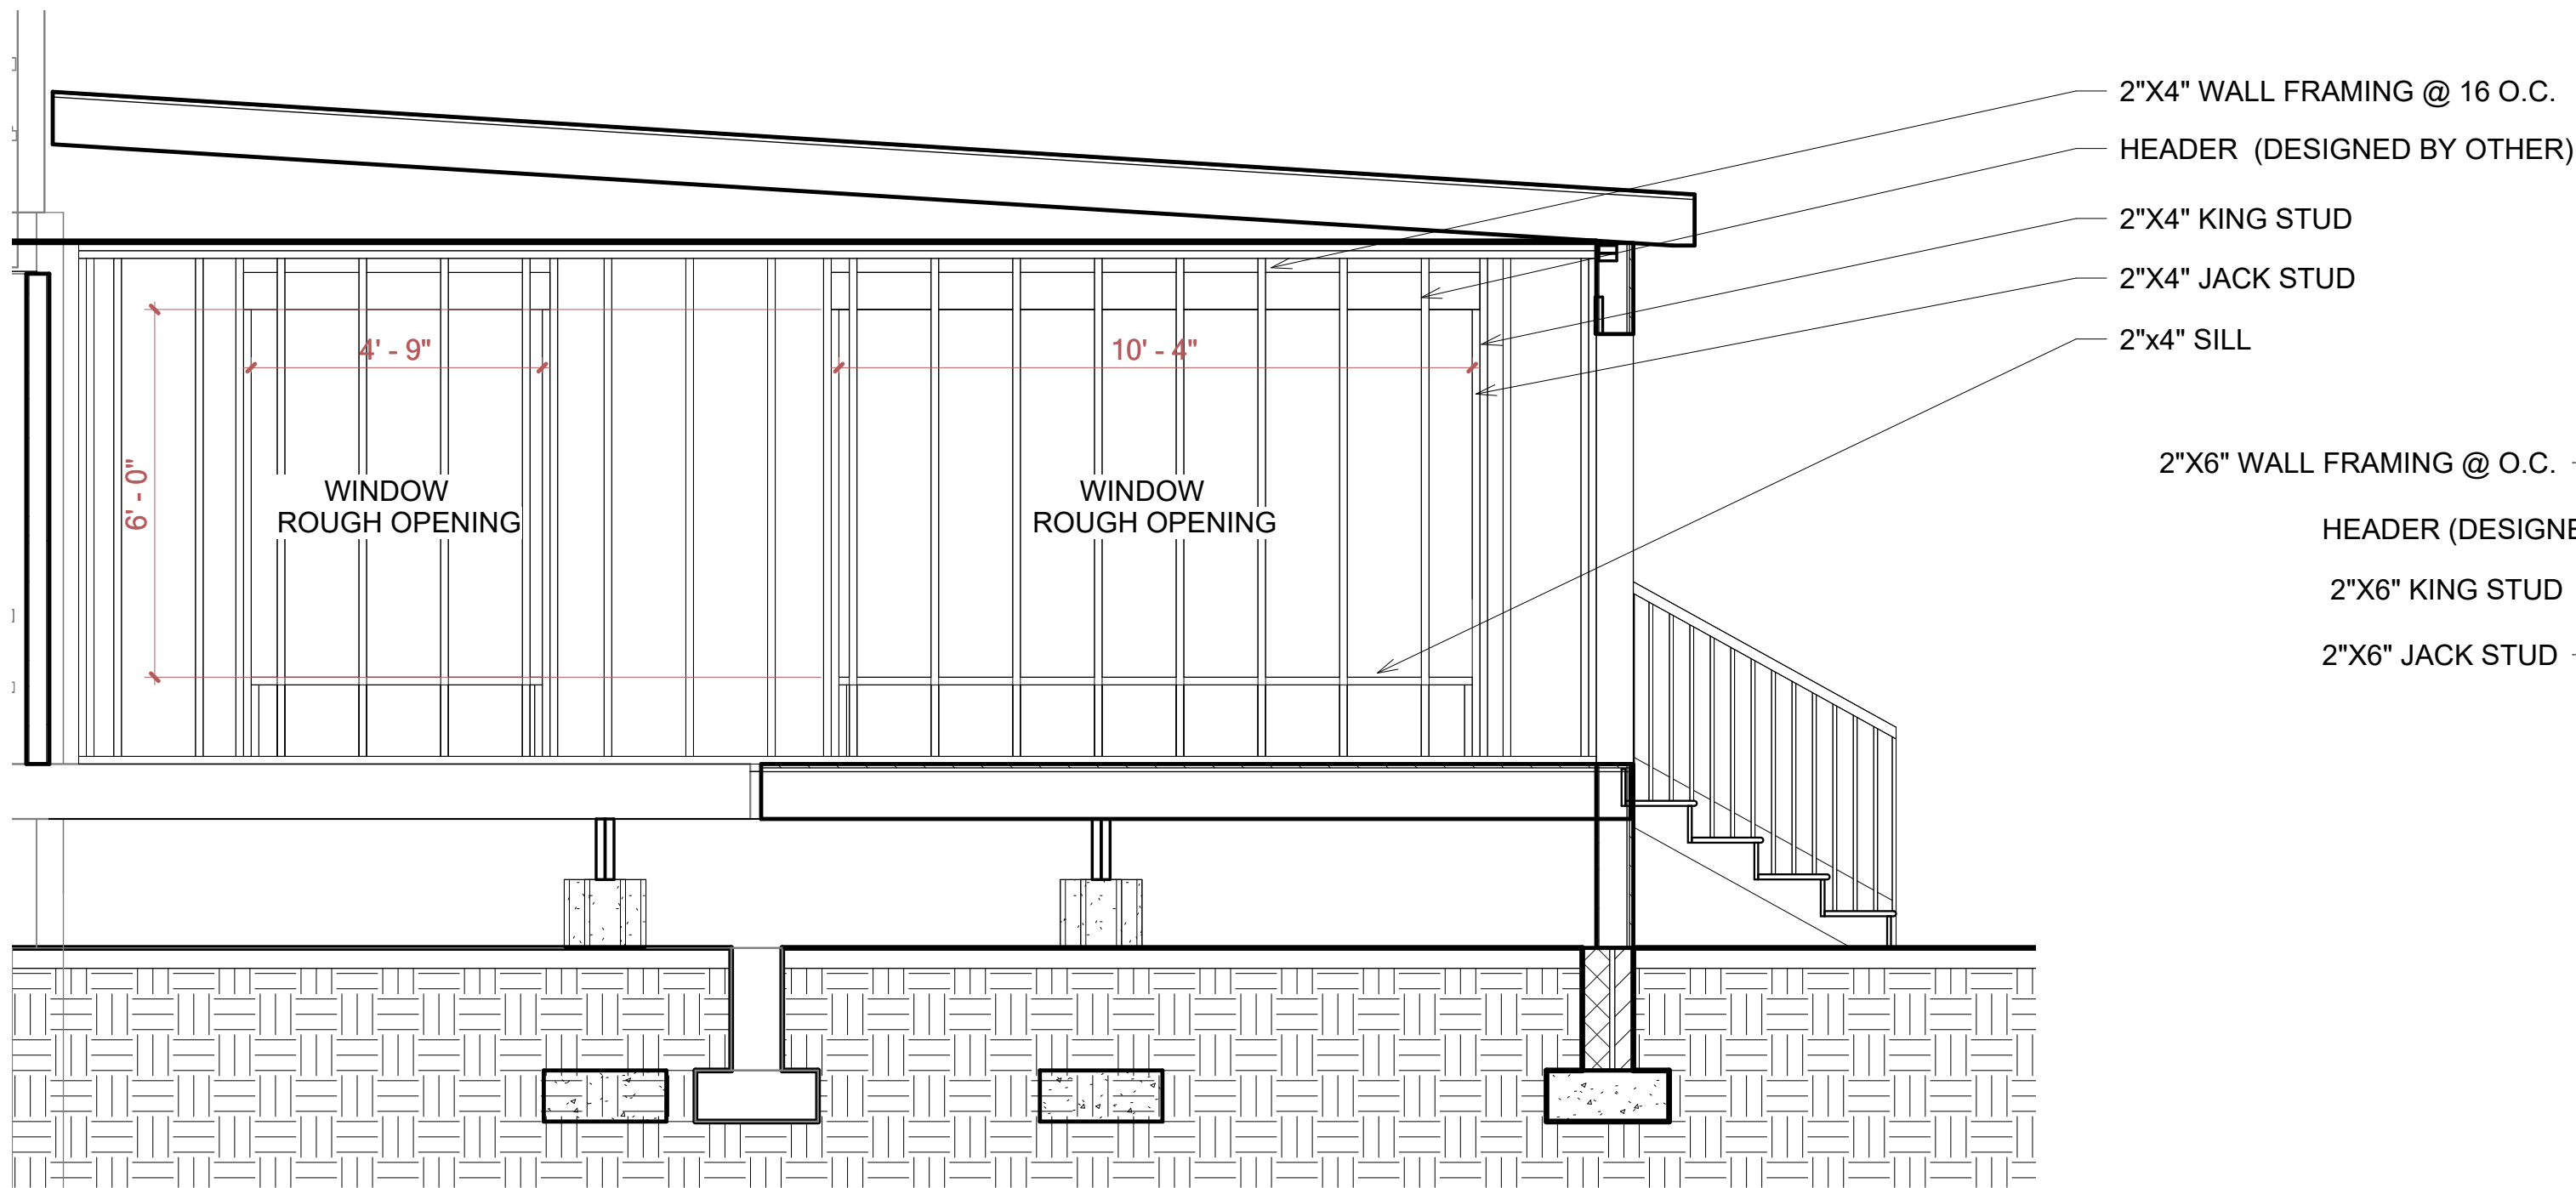

4 LEFT WALL FRAMING DETAIL
3/8" = 1'-0"

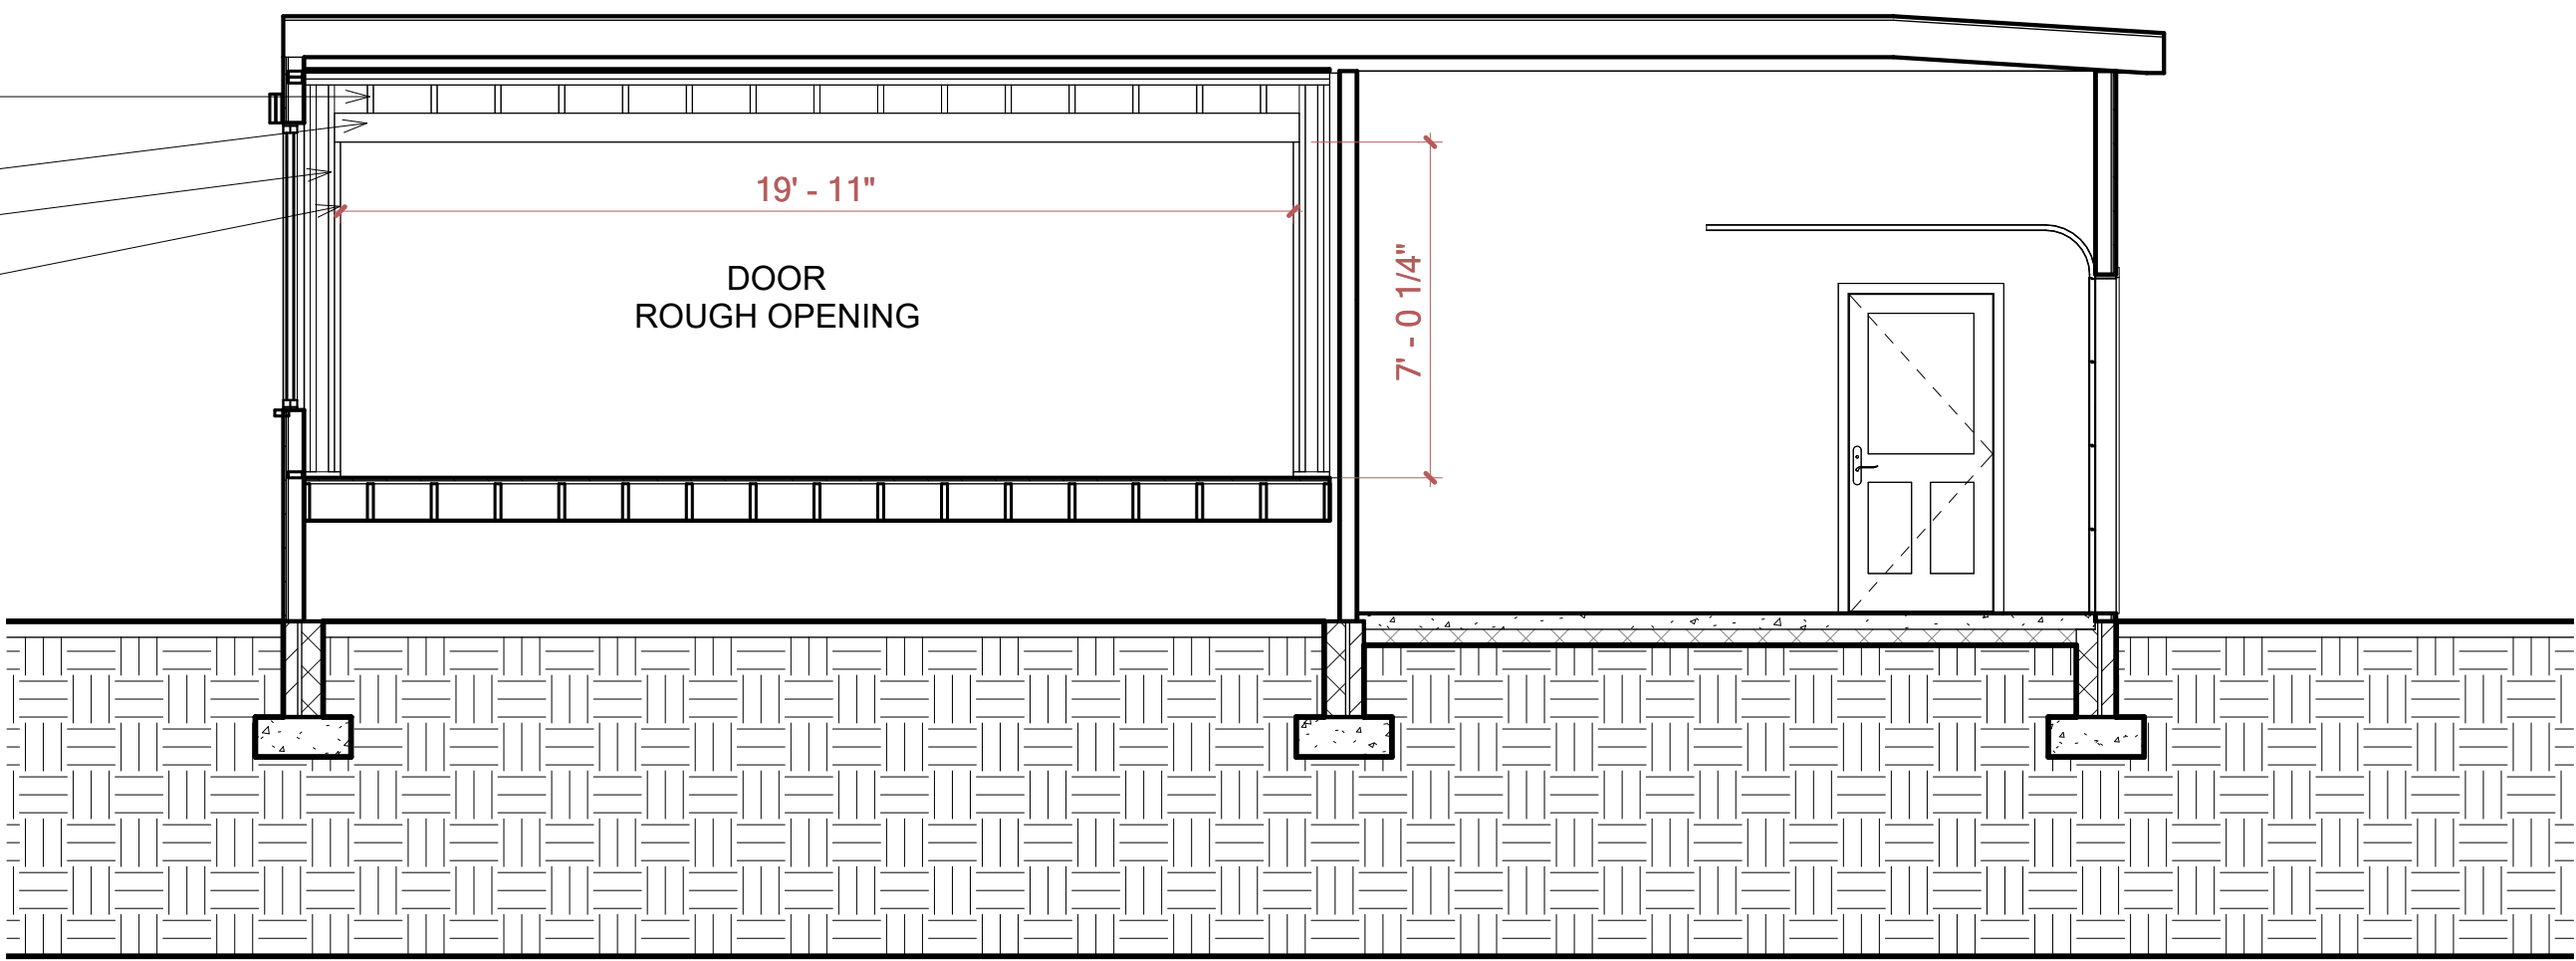

5 REAR WALL FRAMING DETAIL
1/4" = 1'-0"

16 32

Phone
Office Address

SECTIONS

Notes

Rev Num.	Description	Date

Project Name	Project Status	Date	Scale	Sheet Num.
Home Addition	Planning and Permits	07/09/02	As indicated	S.05
Project Adress	Proyect Number	Current Revision	North	File Path
6107 Bay St, Richmond VA 23226	001		↑	C:\Users\gerso\Downloads\6107 Bay St Richmond -- structural -- correction-7-28-25.rvt

e-mail